


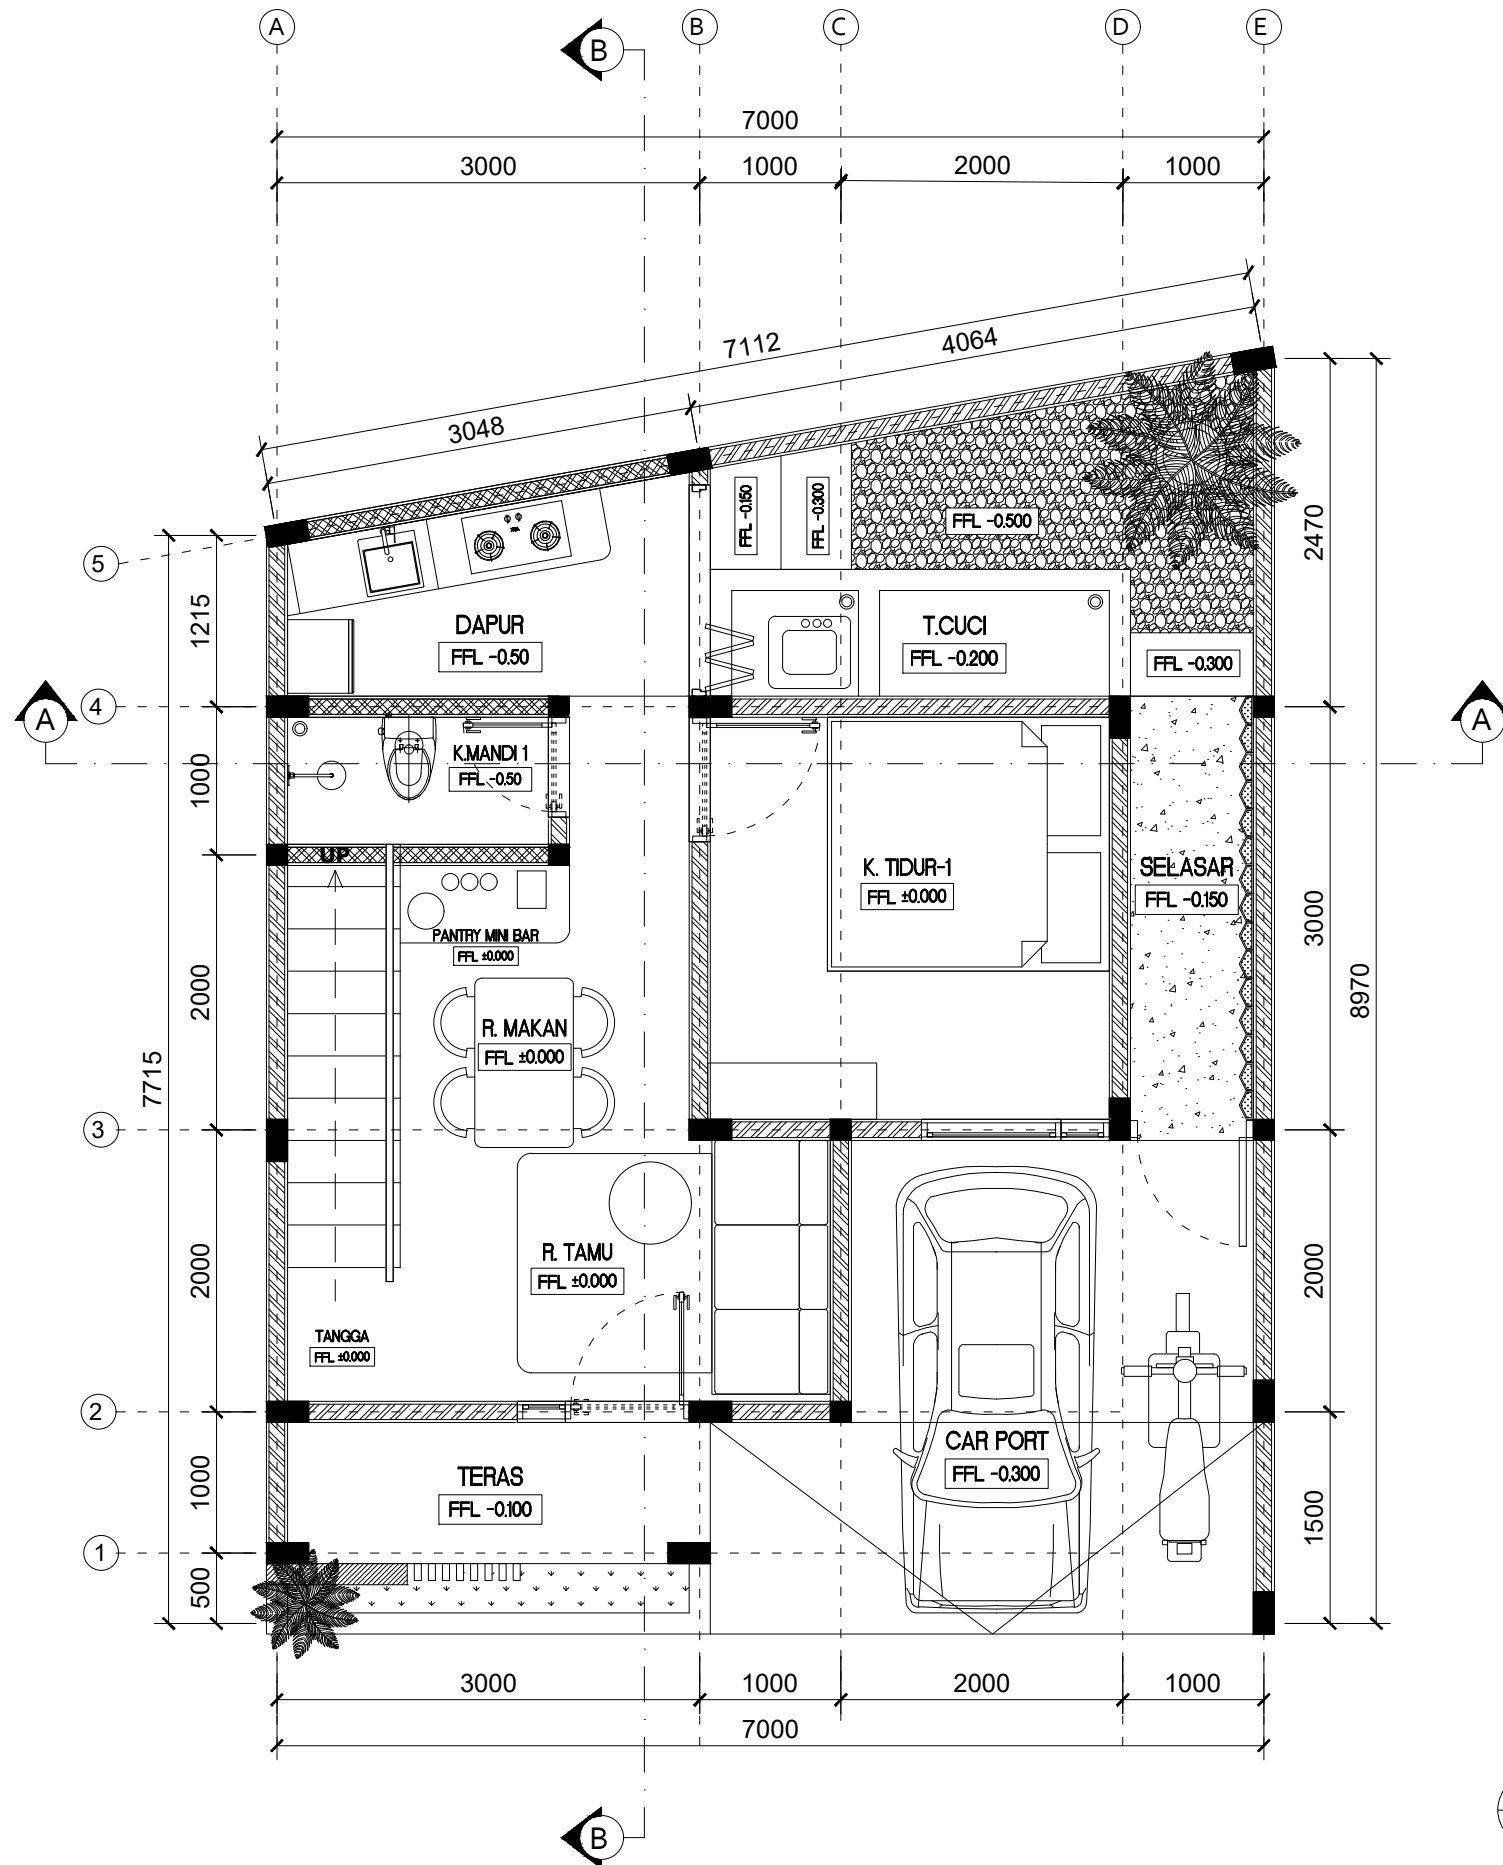

01 DENAH LT.1
ARS S K A L A 1 : 50

KEGIATAN :


PEKERJAAN :

LOKASI :

DIBUAT OLEH :

GAMBAR SKALA

No. Lbr	Jml. Lbr	Kode Gambar
	-	

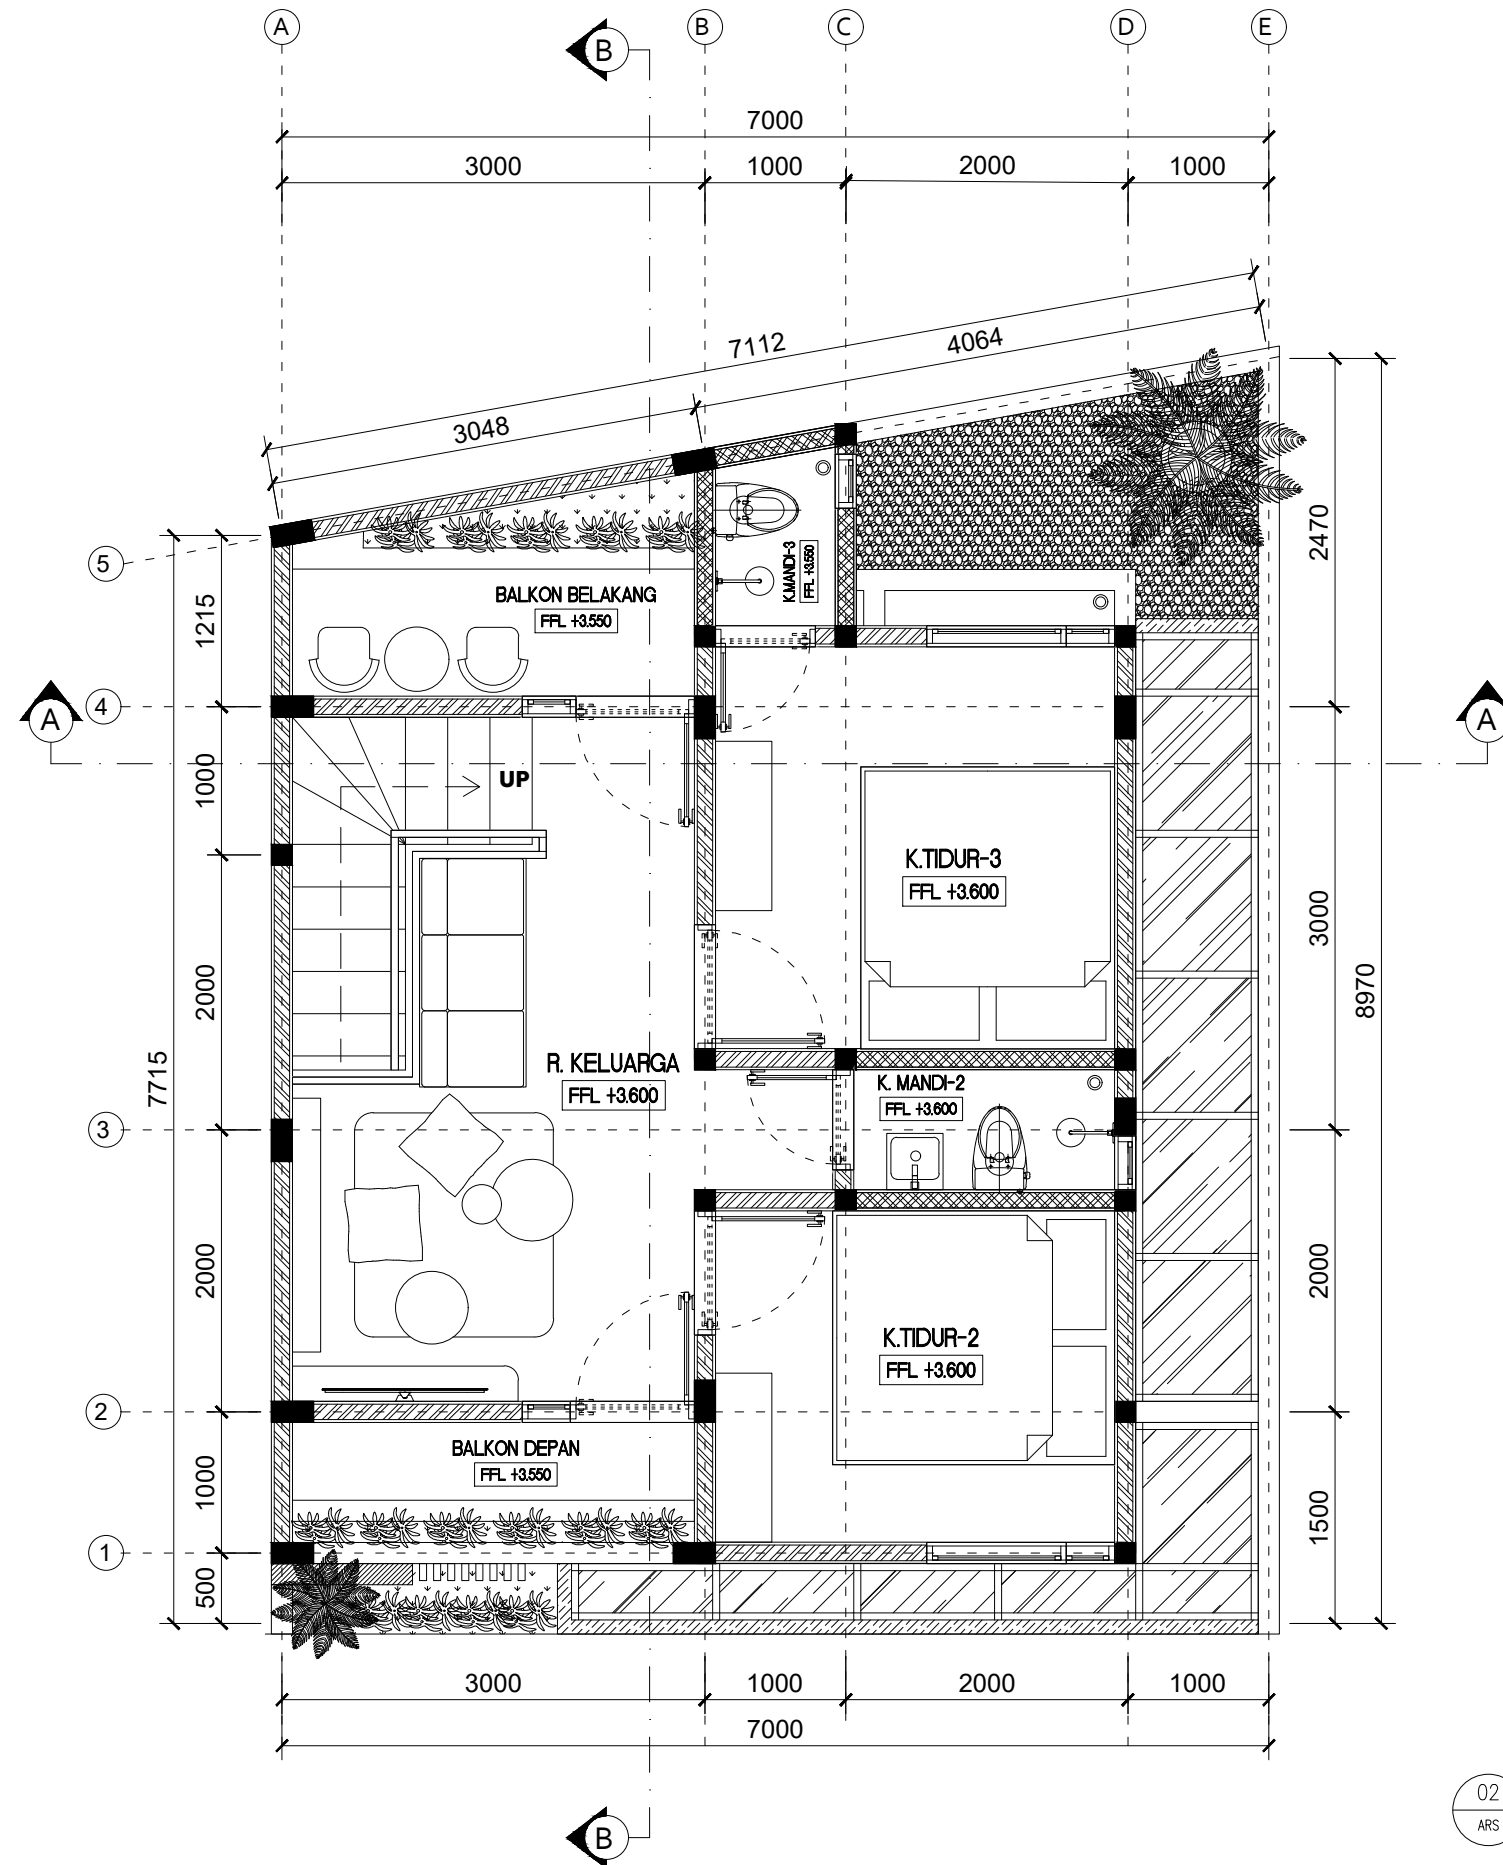

02 DENAH LT.2
ARS S K A L A 1 : 50


KEGIATAN :

PEKERJAAN :

LOKASI :

DIBUAT OLEH :


GAMBAR		SKALA
No. Lbr	Jml. Lbr	Kode Gambar
	-	

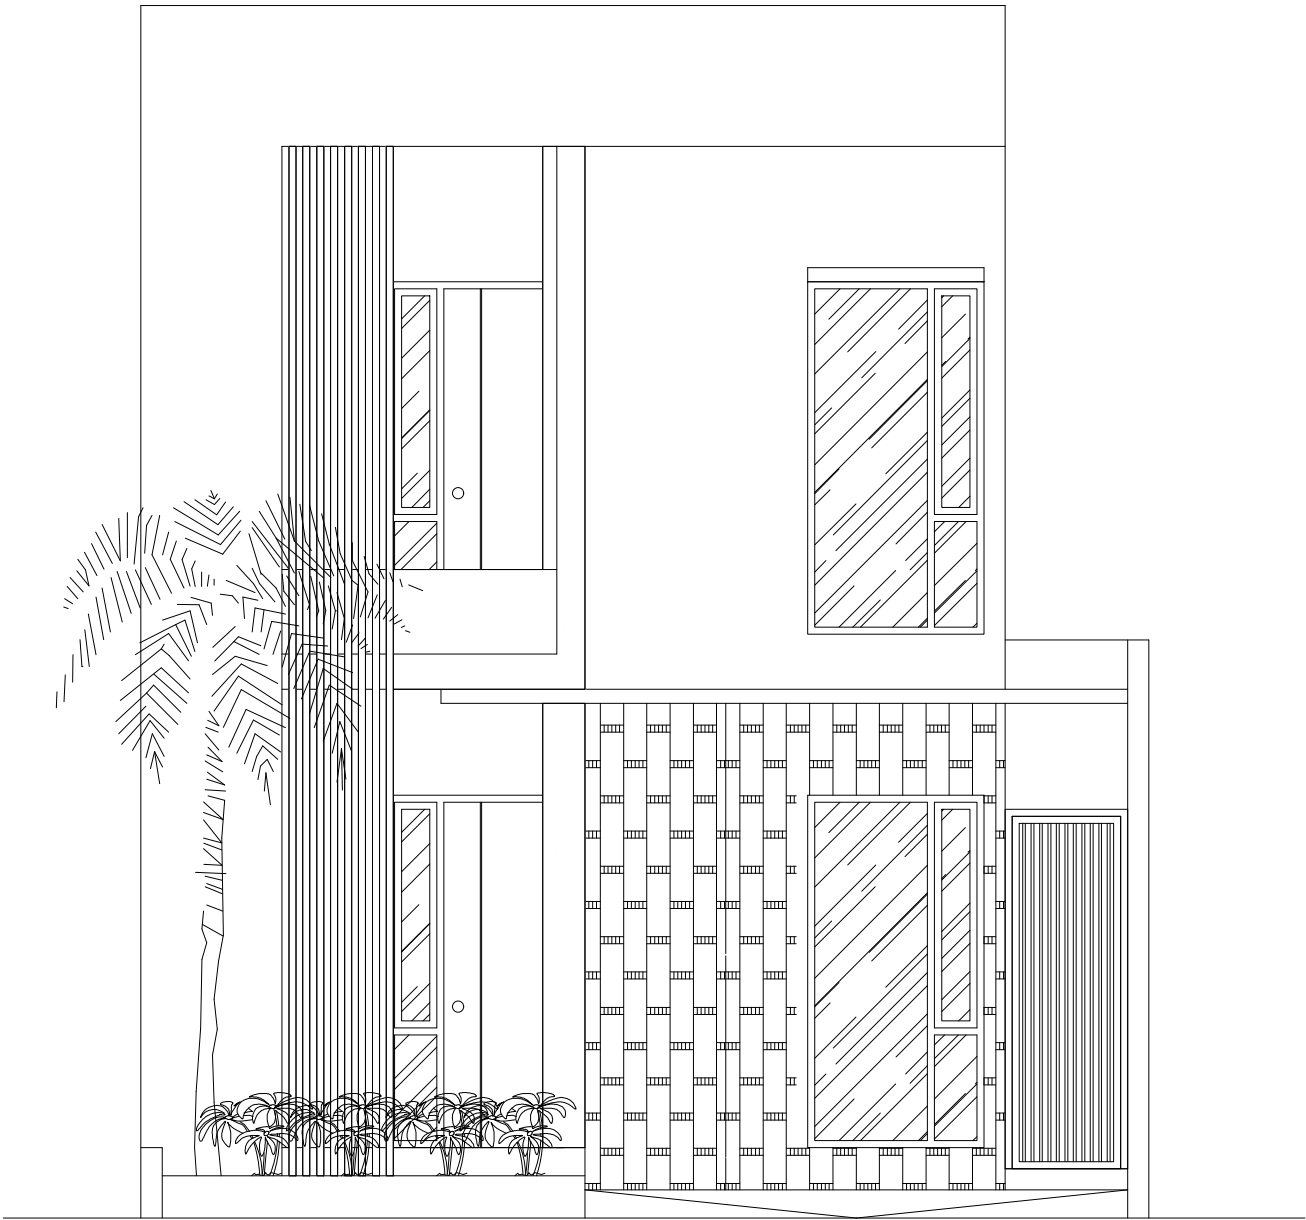


03
ARS

TAMPAK DEPAN
S K A L A 1 : 50

KEGIATAN :		
PEKERJAAN :		
LOKASI :		
DIBUAT OLEH :		
GAMBAR		SKALA
No. Lbr	Jml. Lbr	Kode Gambar
	-	

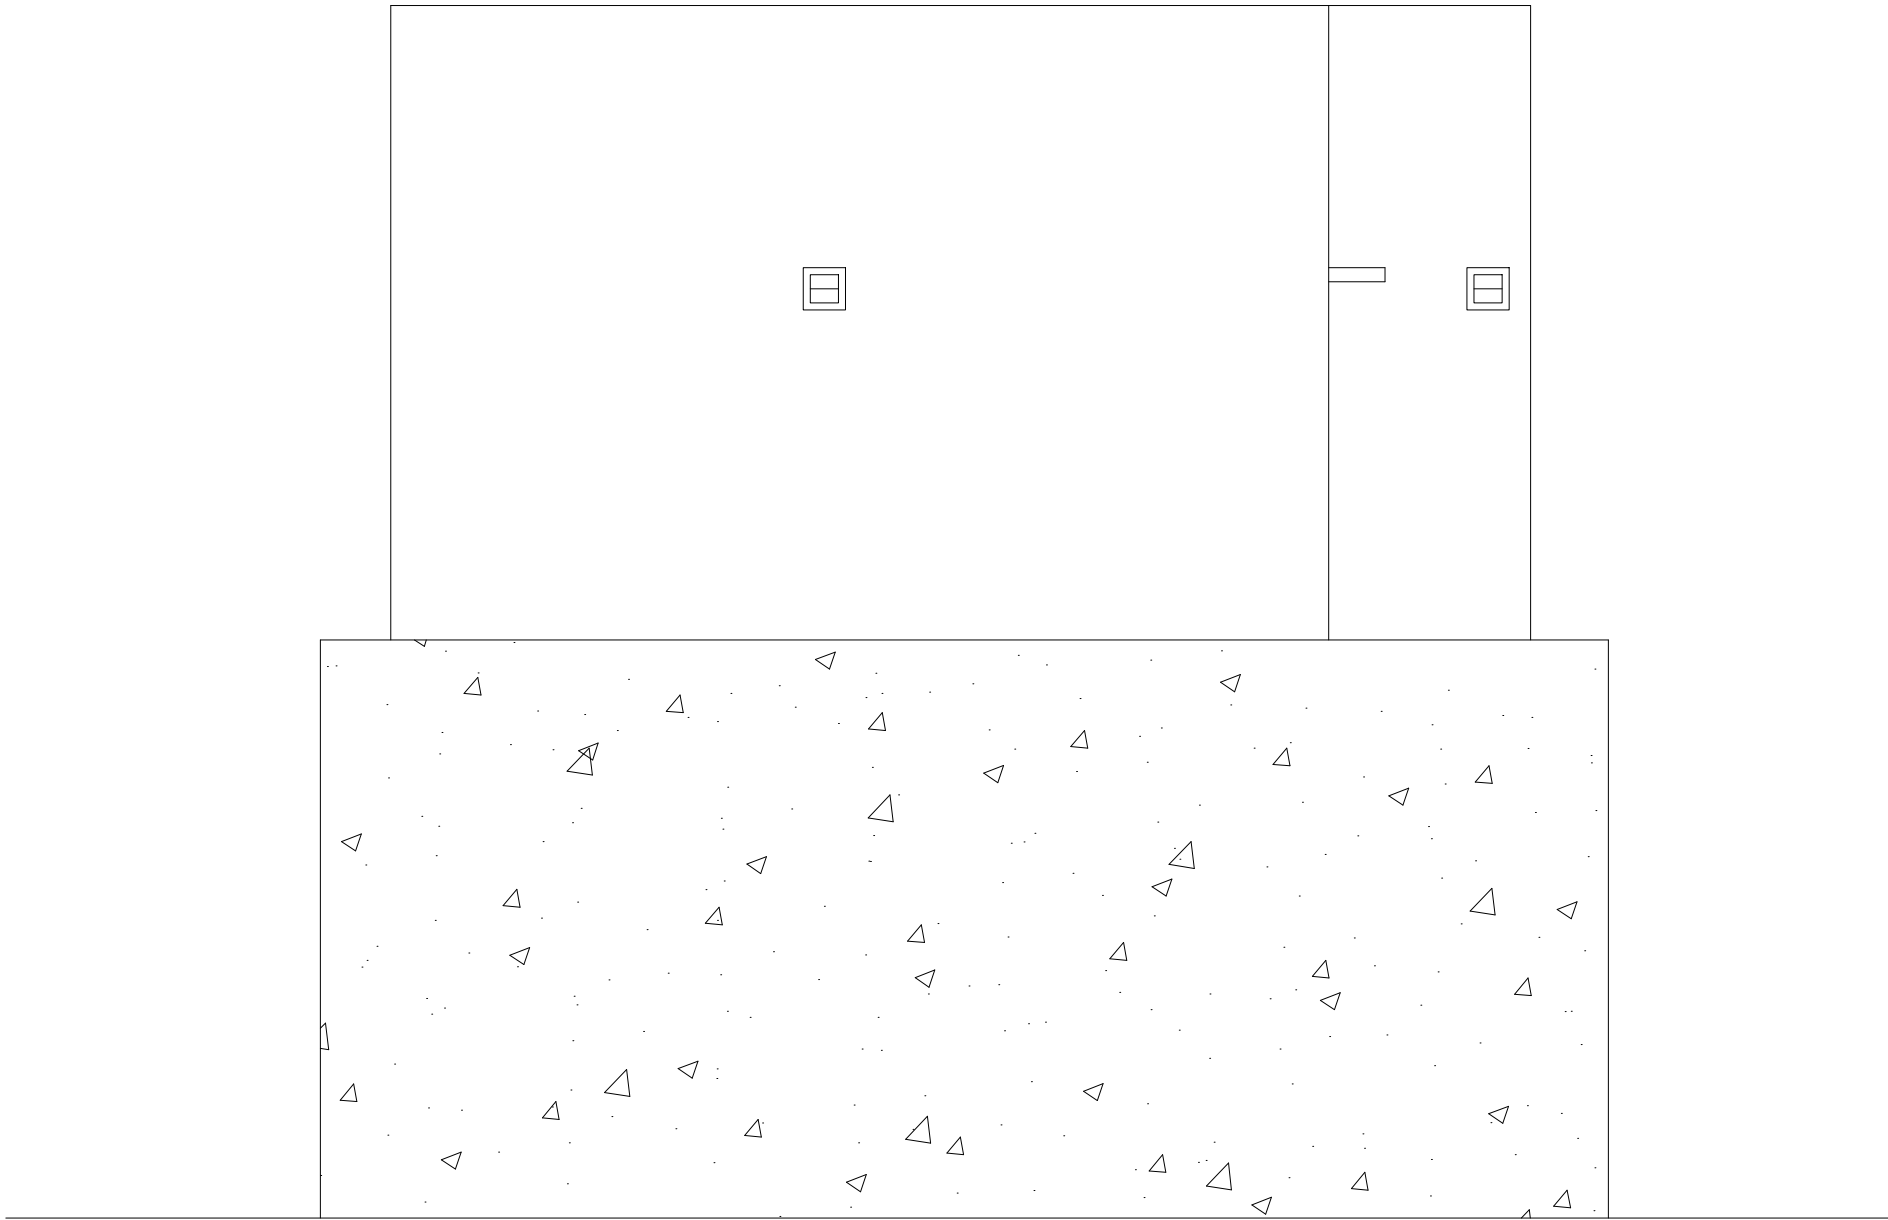

KEGIATAN :		
PEKERJAAN :		
LOKASI :		
DIBUAT OLEH :		
GAMBAR		SKALA
No. Lbr	Jml. Lbr	Kode Gambar
	-	

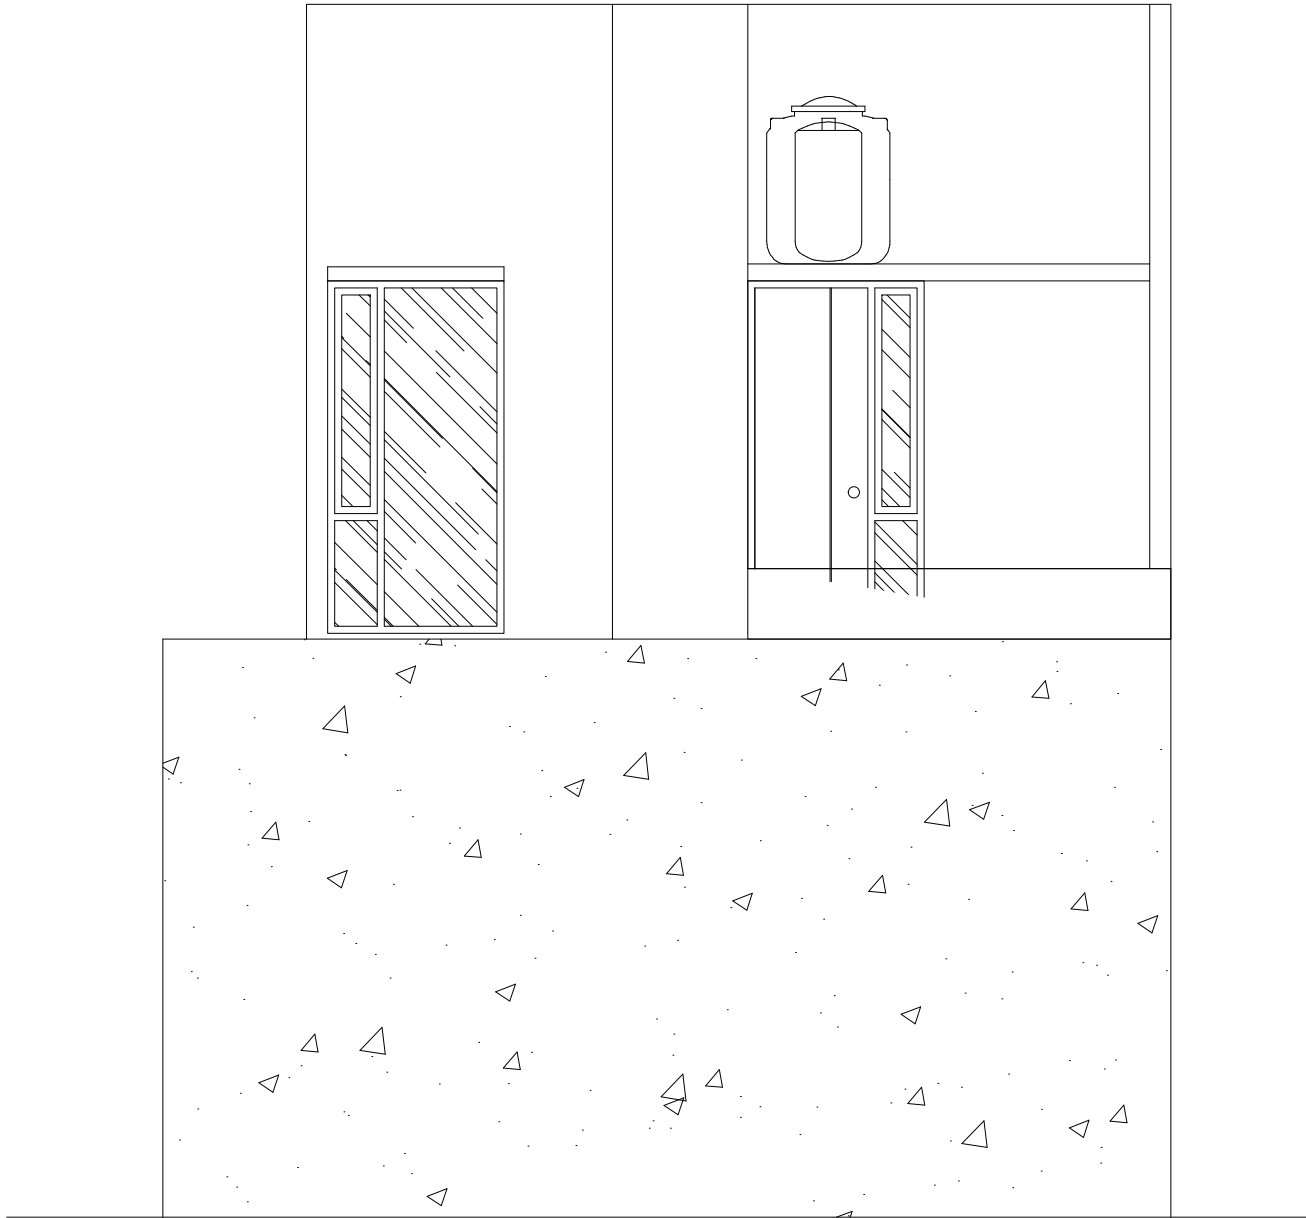


05
ARS

TAMPAK BELAKANG

S K A L A 1 : 50


KEGIATAN :		
PEKERJAAN :		
LOKASI :		
DIBUAT OLEH :		
GAMBAR		SKALA
No. Lbr	Jml. Lbr	Kode Gambar
	-	

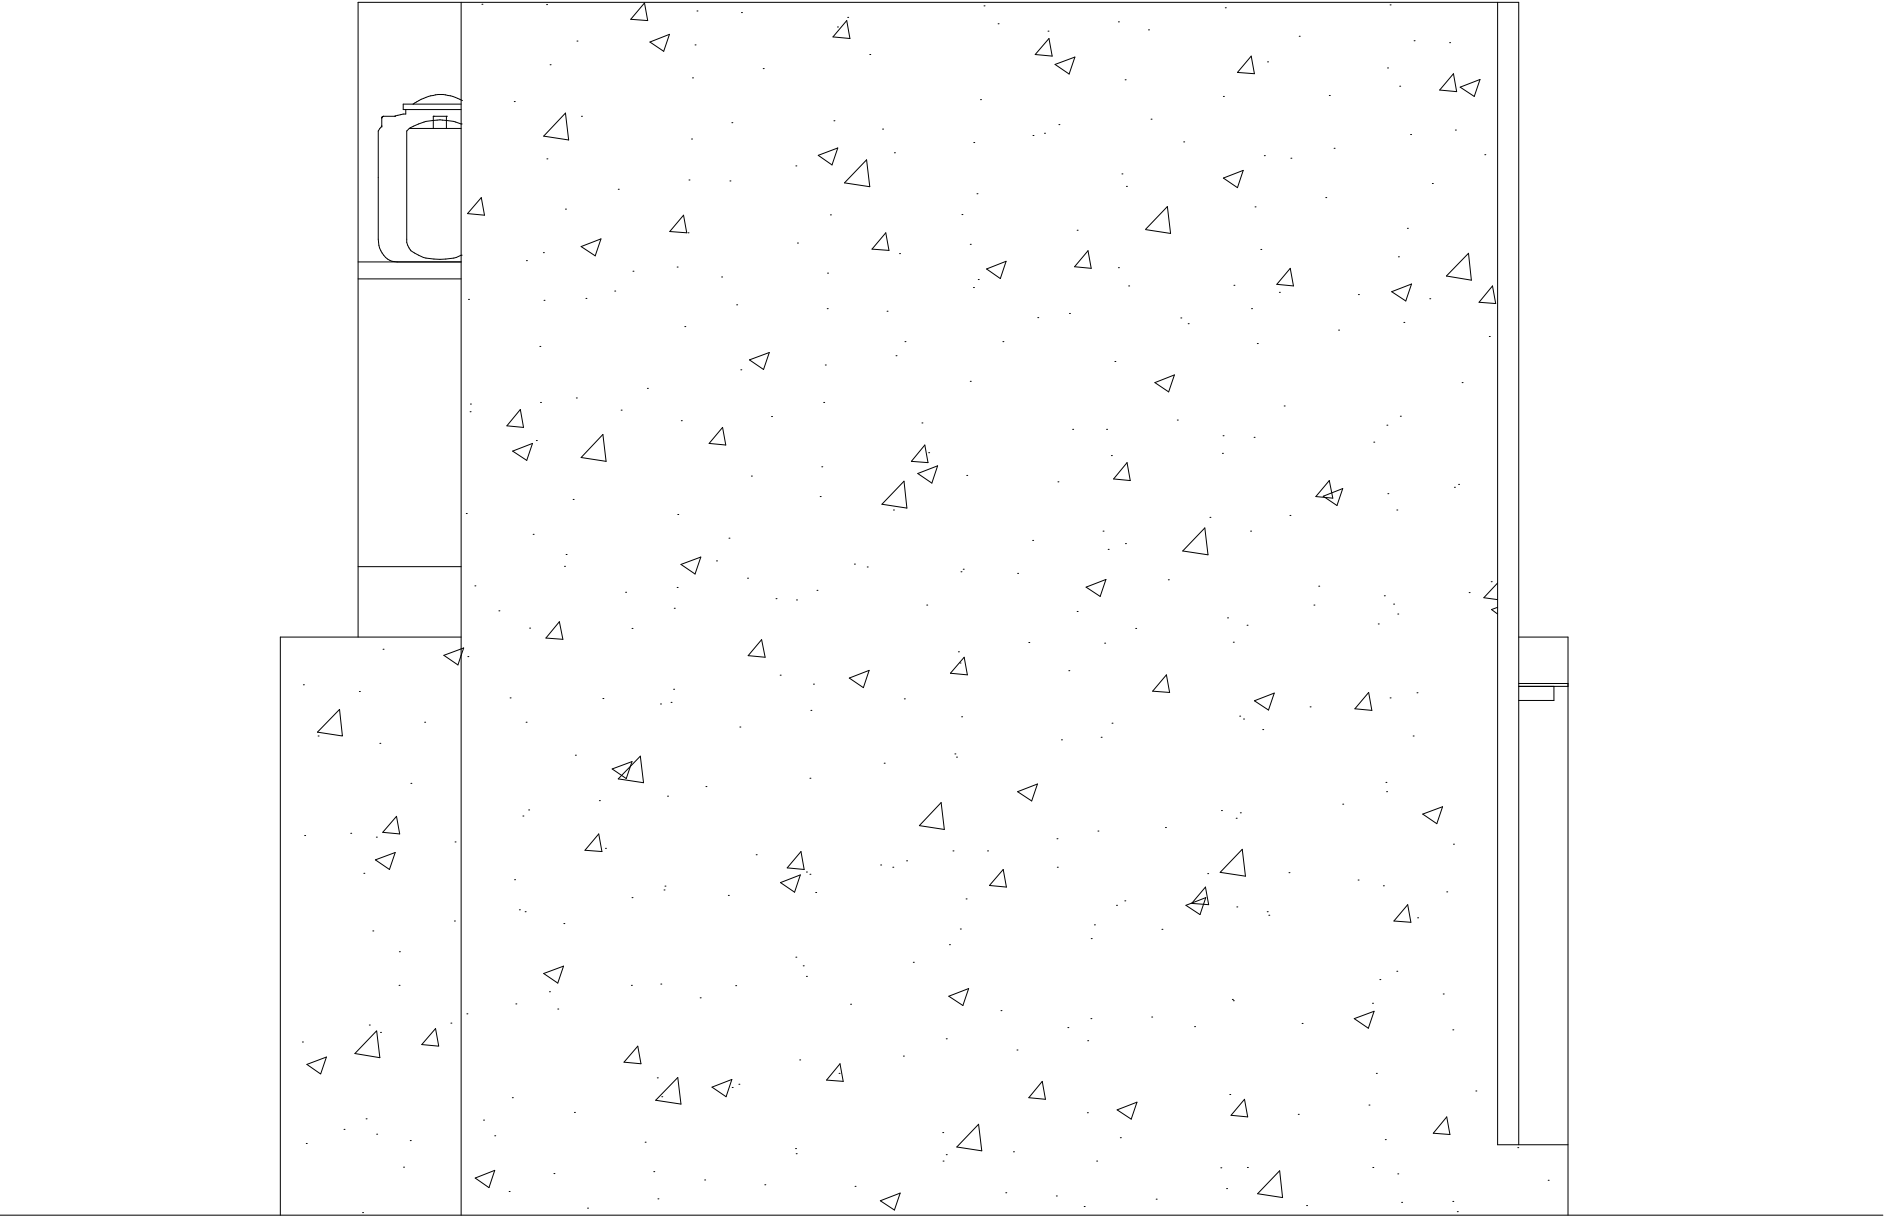

06
ARS


TAMPAK SAMPING KIRI
S K A L A 1 : 50

KEGIATAN :		
PEKERJAAN :		
LOKASI :		
DIBUAT OLEH :		
GAMBAR		SKALA
No. Lbr	Jml. Lbr	Kode Gambar
	-	

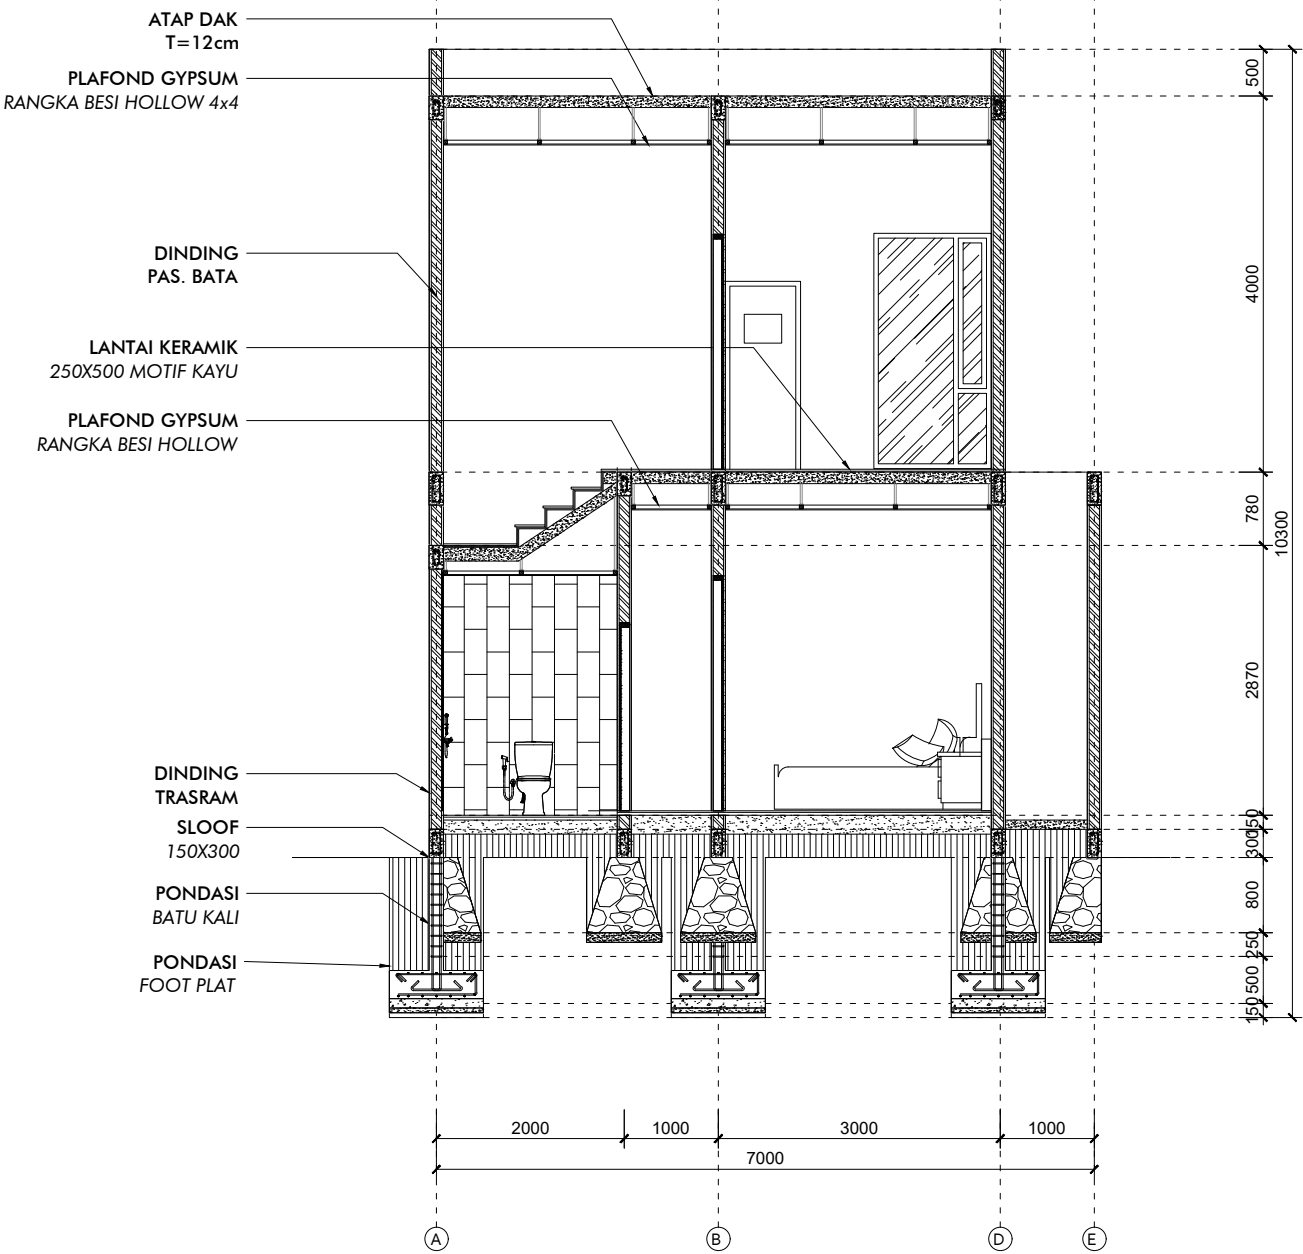

07 POTONGAN A-A
ARS S K A L A 1 : 75

KEGIATAN :		
PEKERJAAN :		
LOKASI :		
DIBUAT OLEH :		
GAMBAR		SKALA
No. Lbr	Jml. Lbr	Kode Gambar
	-	

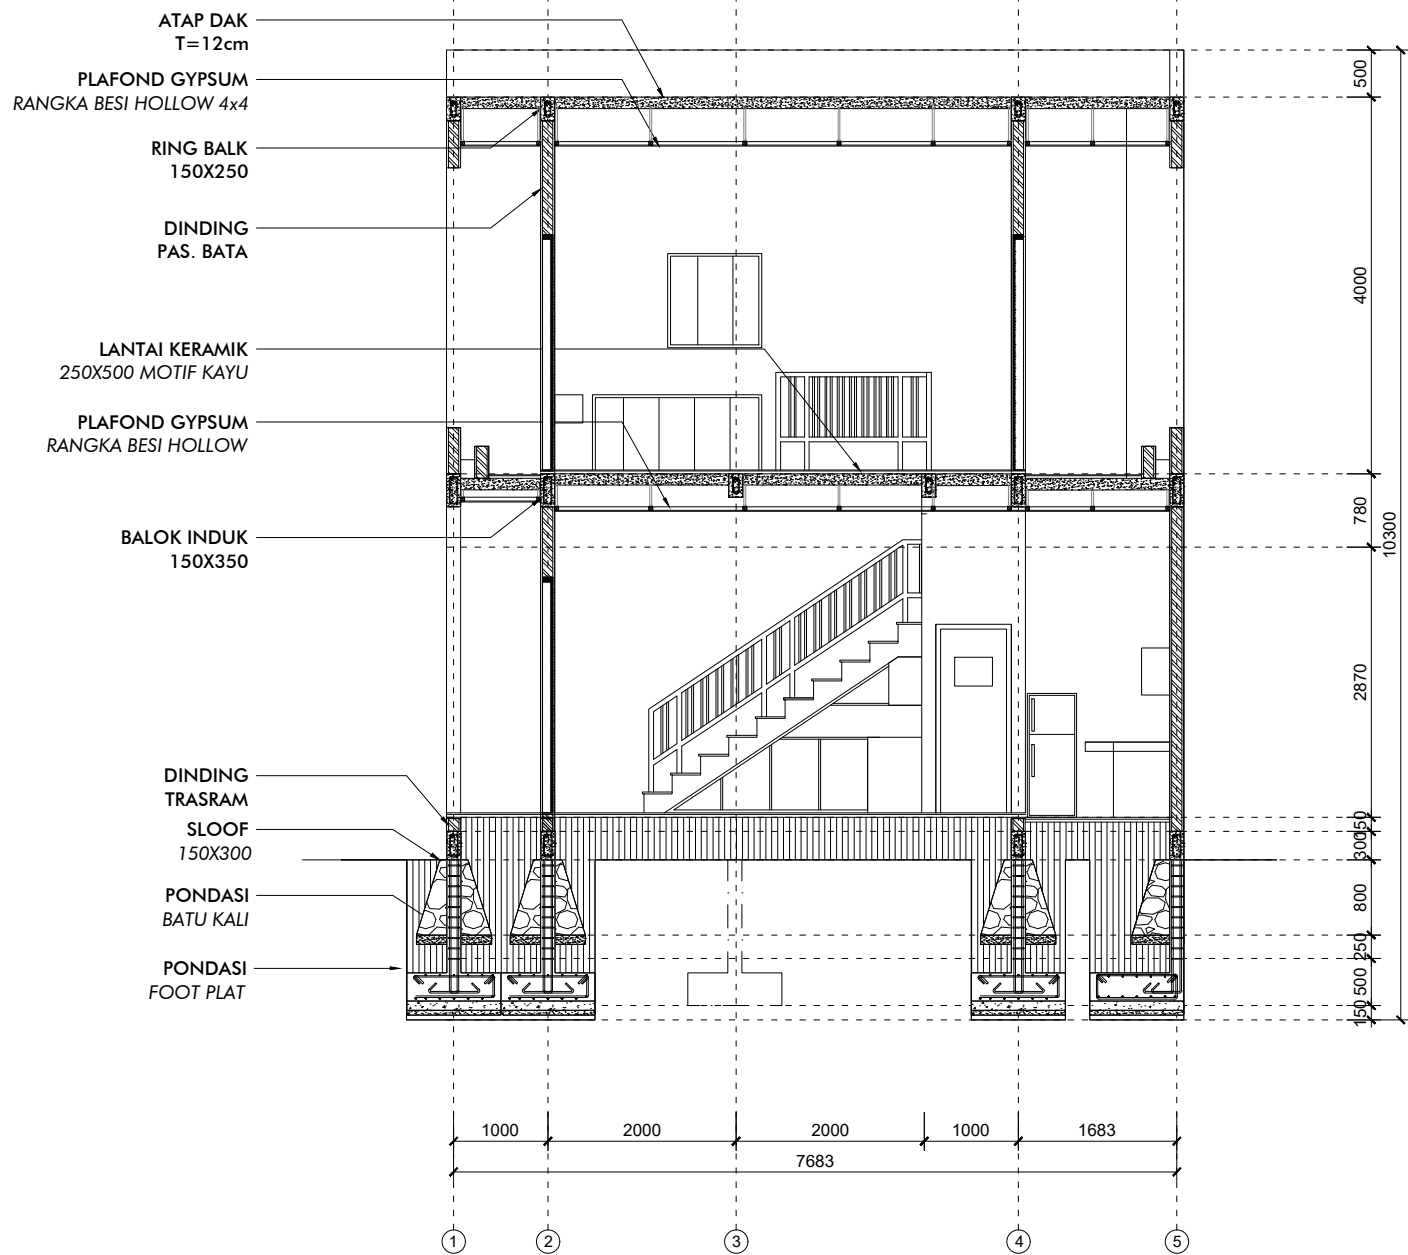

08 POTONGAN B-B
ARS SKALA 1 : 75

KEGIATAN :


PEKERJAAN :

LOKASI :


DIBUAT OLEH :

GAMBAR SKALA

No. Lbr	Jml. Lbr	Kode Gambar
	-	

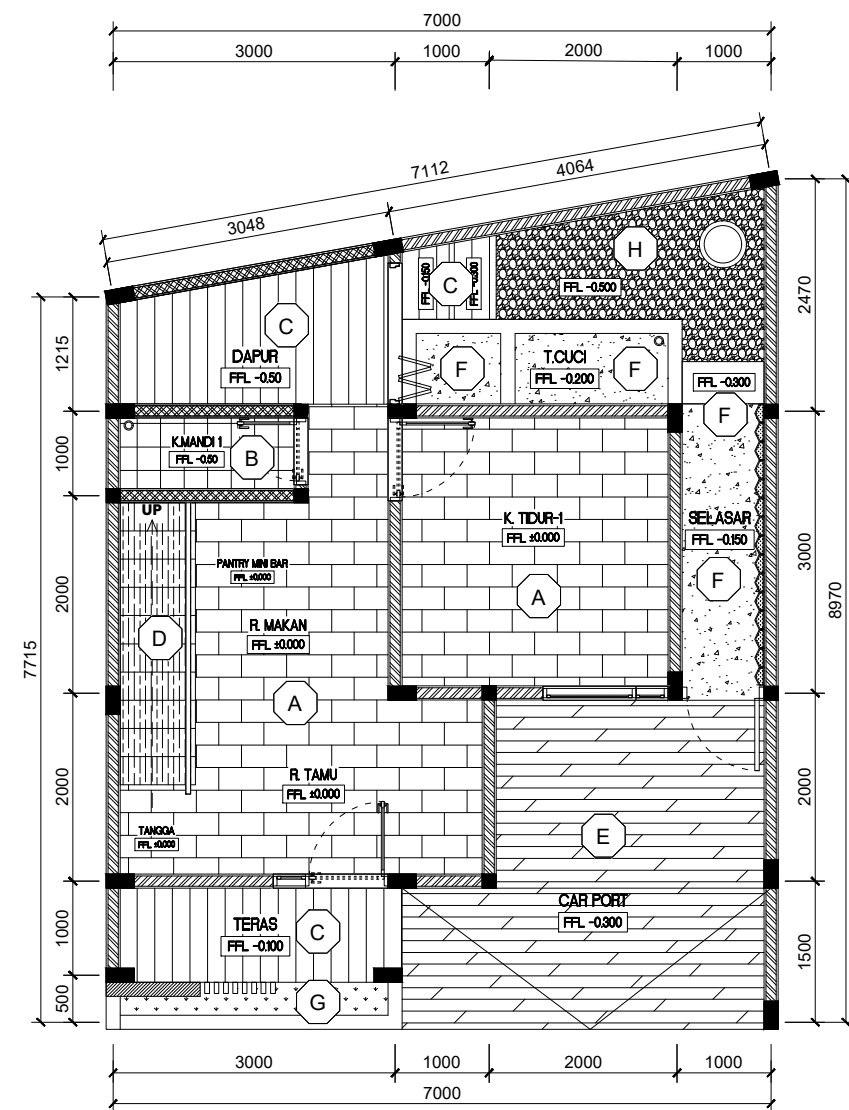

0
ARS
DENAH LT.1
1: 75

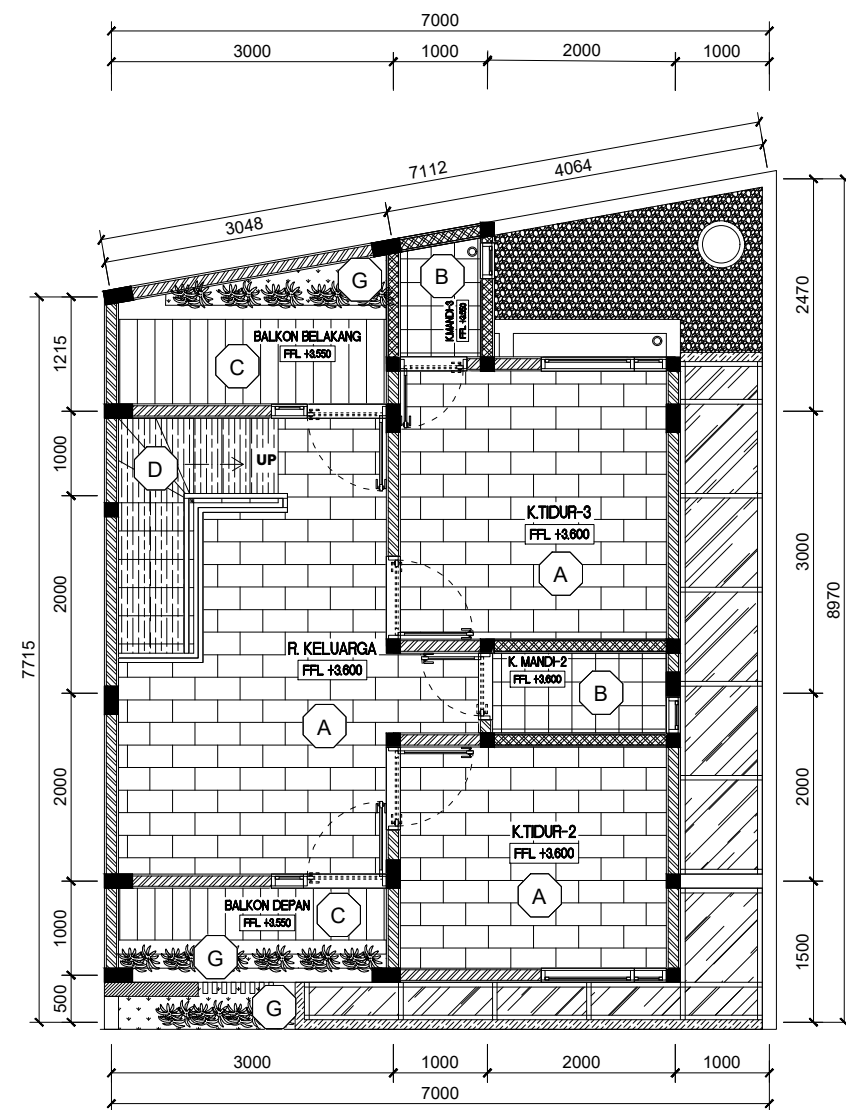

0
ARS
DENAH LT.2
1: 75

KETERANGAN

- A KERAMIK POTIF KAYU
- B KERAMIK 20X20 CM GREY UNPOLISHED
- C KERAMIK MOTIF KAYU UNPOLISHED
- D TRAP TANGGA KAYU
- E ACIAN KASAR TALI AIR 1000X750 CM
- F ACIAN HALUS
- G RUMPUT GAJAH MINI
- H KRIKIL

09
ARS
DENAH RENC. LANTAI
SKALA 1 : 75

KEGIATAN :


PEKERJAAN :

LOKASI :


DIBUAT OLEH :

GAMBAR SKALA

No. Lbr Jml. Lbr Kode Gambar

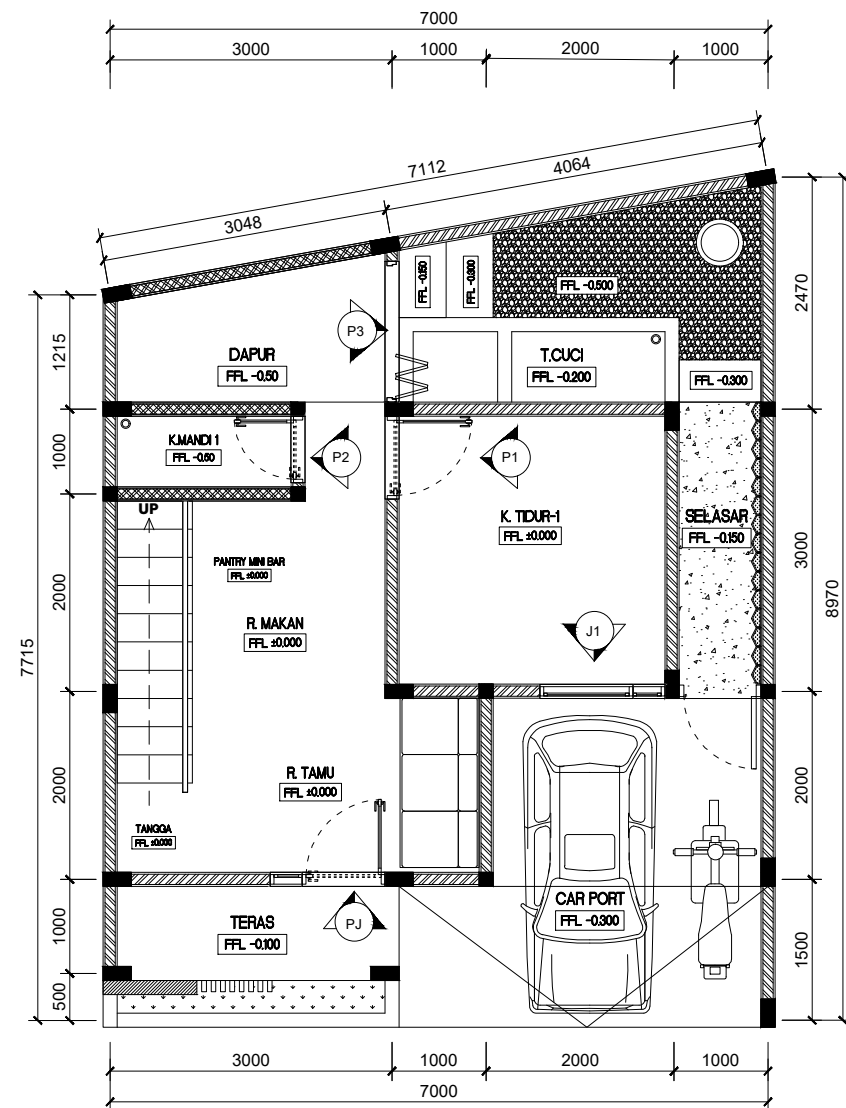

0
ARS
DENAH LT.1
1:75

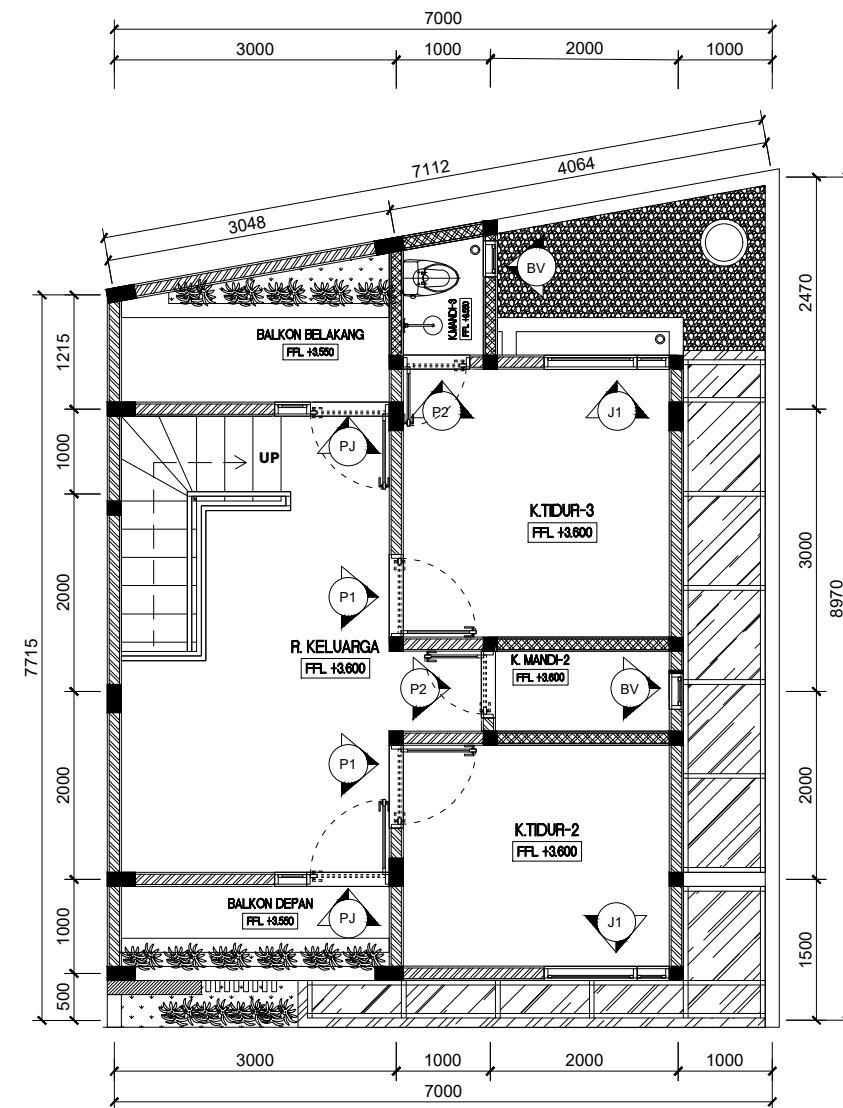

0
ARS
DENAH LT.2
1:75

10
ARS
DENAH PINTU&JENDELA
SKALA 1:75


KEGIATAN :

PEKERJAAN :


LOKASI :

DIBUAT OLEH :

GAMBAR		SKALA
No. Lbr	Jml. Lbr	Kode Gambar
	-	

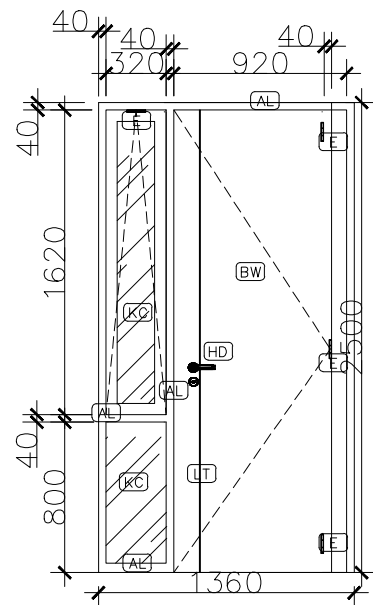


28
ARS
TAMPAK DEPAN PJ1
1:30

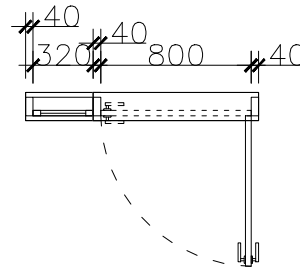

30
ARS
DENAH PJ1
1:30


DETAIL PINTU TYPE PJ
Jumlah : 1

UKURAN LUAR	1360 x 2500
AL	RANGKA KUSEN ALMUNIUH HITAM
DAUN PINTU	T. 4CM RANGKA MERANTI OVEN, LAPIS PANIL BLOCK BOARD T: 6MM
BW	BLOCK BOARD T: 6 MM FIN. KAYU MELAMIN
BB	BLOCK BOARD T: 6 MM FIN. DUCO WARNA ABU-ABU TUA
HD	HANDLE
TL	LIST TALI AIR
E	ENGSEL
KC	KACA BENING 5 MM

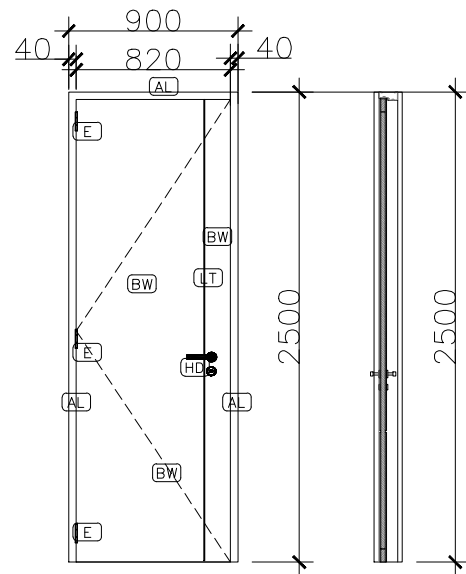

29
ARS
TAMPAK DEPAN P1
1:30


29
ARS
TAMPAK SAMPING P1
1:30

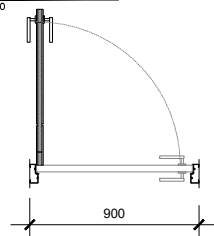

29
ARS
DENAH P1
1:30


DETAIL PINTU TYPE P1
Jumlah : 4

UKURAN LUAR	900 x 2500
AL	RANGKA KUSEN ALMUNIUH HITAM
DAUN PINTU	T. 4CM RANGKA MERANTI OVEN, LAPIS PANIL BLOCK BOARD T: 6MM
BW	BLOCK BOARD T: 6 MM FIN. KAYU MELAMIN
BB	BLOCK BOARD T: 6 MM FIN. DUCO WARNA ABU-ABU TUA
HD	HANDLE
TL	LIST TALI AIR
E	ENGSEL

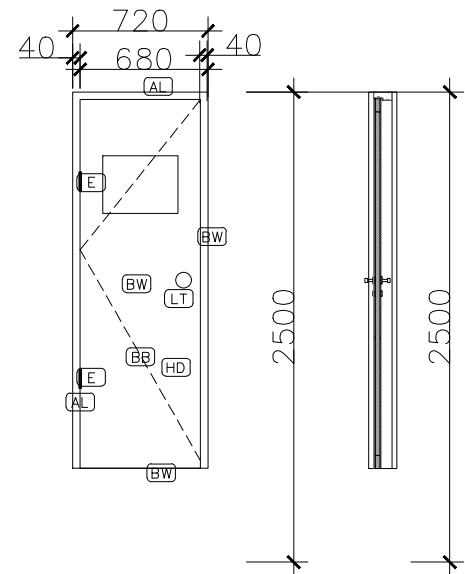

29
ARS
TAMPAK DEPAN PK
1:30

29
ARS
TAMPAK SAMPING PK
1:30

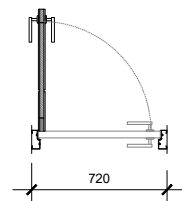

29
ARS
DENAH PK
1:30

DETAIL PINTU TYPE P2
Jumlah : 3

UKURAN LUAR	720 x 2500
AL	RANGKA KUSEN ALMUNIUH HITAM
DAUN PINTU	T. 4CM RANGKA MERANTI OVEN, LAPIS PANIL BLOCK BOARD T: 6MM
BW	BLOCK BOARD T: 6 MM FIN. KAYU MELAMIN
BB	BLOCK BOARD T: 6 MM FIN. DUCO WARNA ABU-ABU TUA
HD	HANDLE
TL	LIST TALI AIR
E	ENGSEL



DETAIL PINTU&JENDELA
S K A L A 1 : 30

KEGIATAN :

PEKERJAAN :

LOKASI :

DIBUAT OLEH :



GAMBAR

SKALA

No. Lbr


Jml. Lbr

Kode Gambar

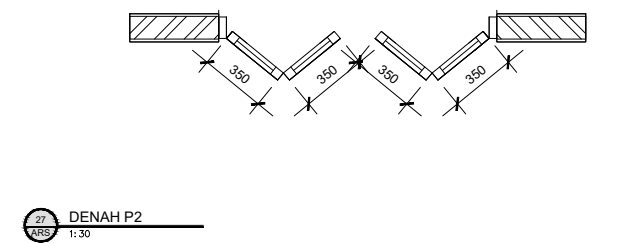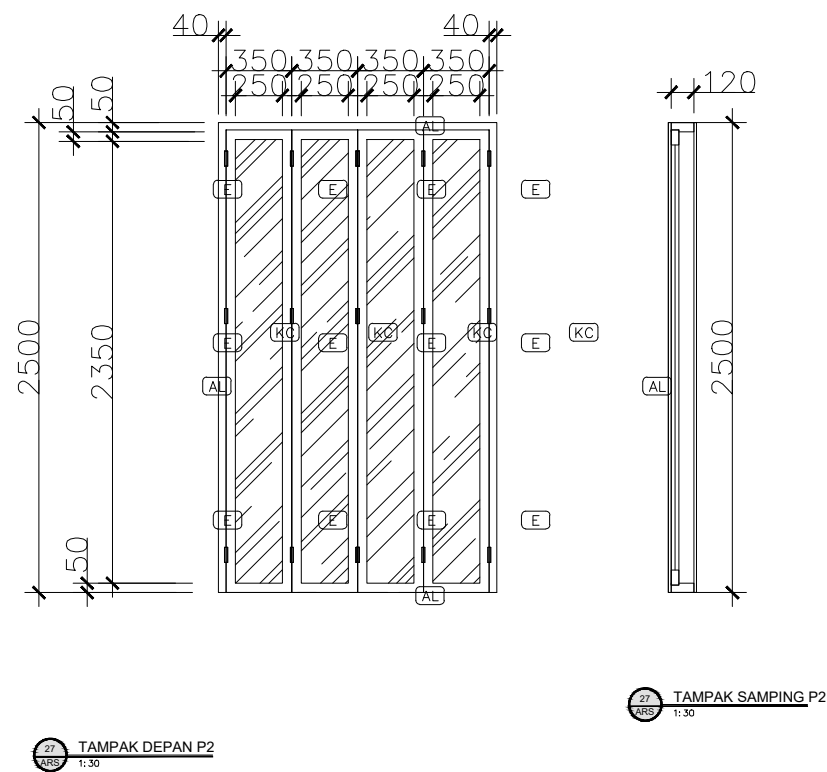


DETAIL PINTU TYPE P2
Jumlah : 1

UKURAN LUAR	2800 x 2500
AL	RANGKA KUSEN ALMUNUM BLACK
HD	HANDLE
TL	LIST TALI AIR
E	ENGSEL
KC	KACA BENING 5 MM

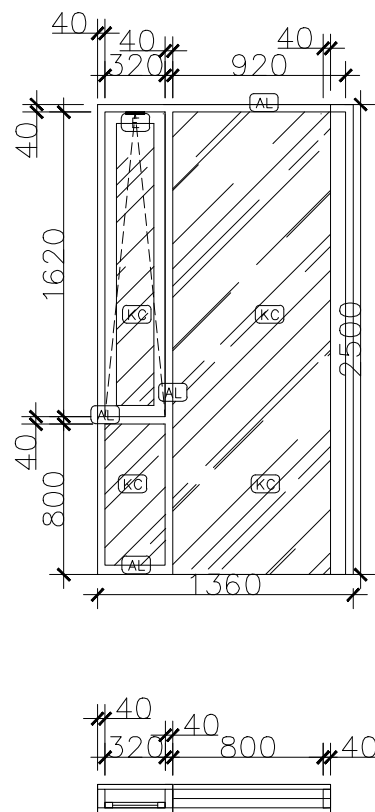

DETAIL JENDELA J1
Jumlah : 1


UKURAN LUAR	1200 x 2500
AL	RANGKA KUSEN UPVC 4" BLACK
KC	KACA BENING 5 MM
E	ENGSEL

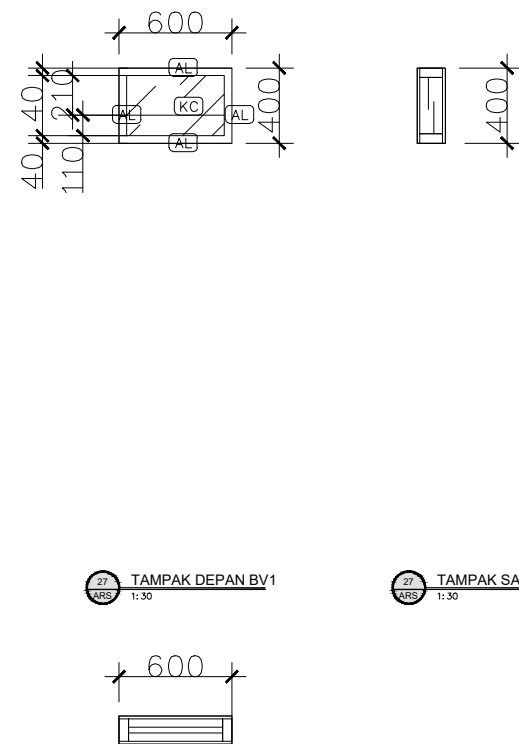


DETAIL BOVEN 2 BV2
Jumlah : 1

UKURAN LUAR	600 x 400
AL	RANGKA KUSEN ALMUNUM BLACK
KC	KACA BENING 5 MM

KEGIATAN :		
PEKERJAAN :		
LOKASI :		
DIBUAT OLEH :		
GAMBAR		SKALA
No. Lbr	Jml. Lbr	Kode Gambar
	-	

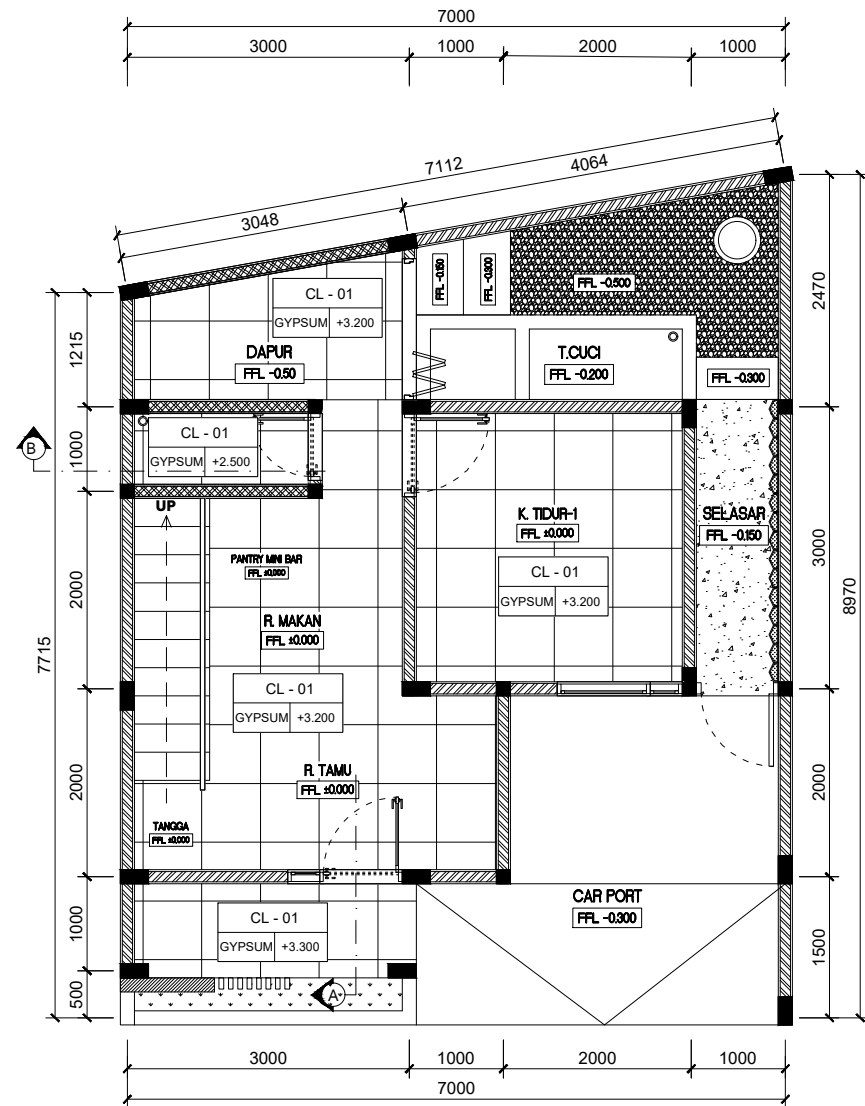

0
ARS
DENAH LT.1
1: 75

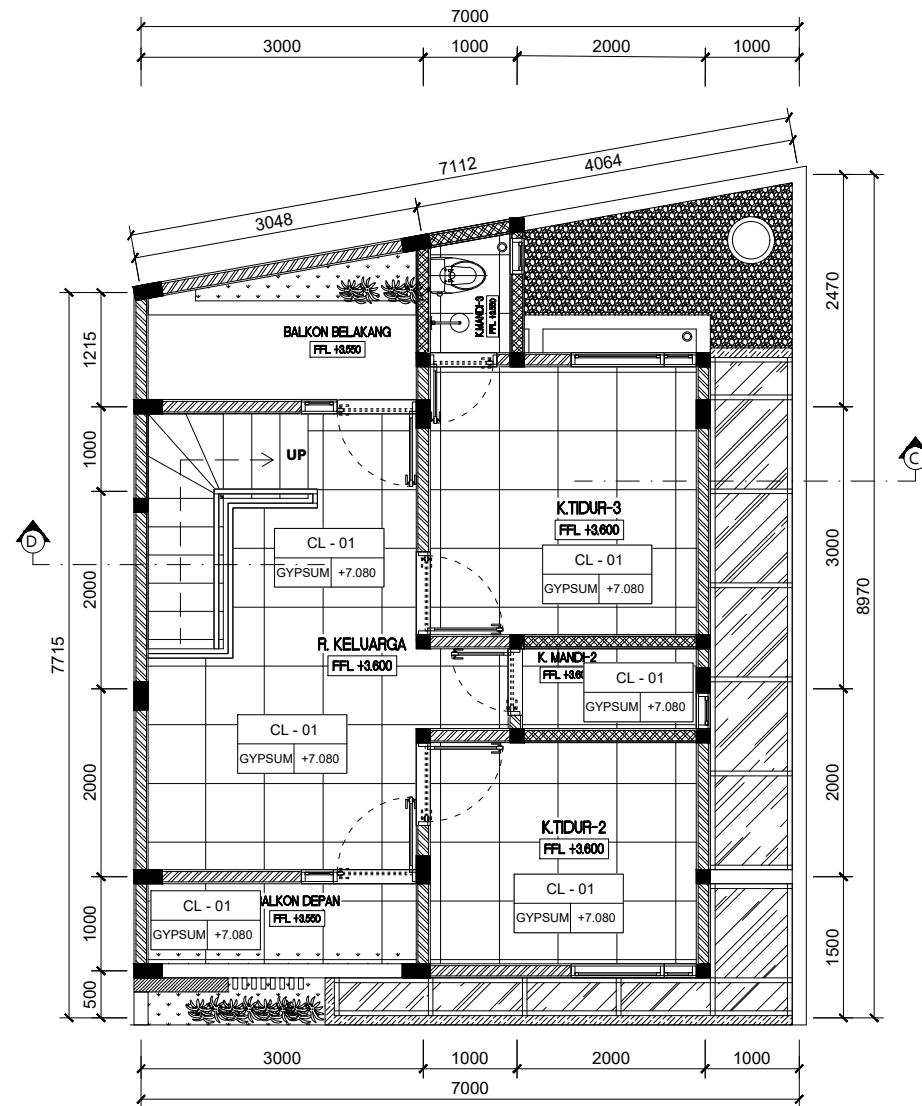

0
ARS
DENAH LT.2
1: 75

KETERANGAN

CL-01 PLAFON GYPSUM RANGKA BESI
HOLLOW

10
ARS
DENAH PLAFOND
SKALA 1 : 75

KEGIATAN :


PEKERJAAN :

LOKASI :


DIBUAT OLEH :

GAMBAR SKALA


No. Lbr Jml. Lbr Kode Gambar

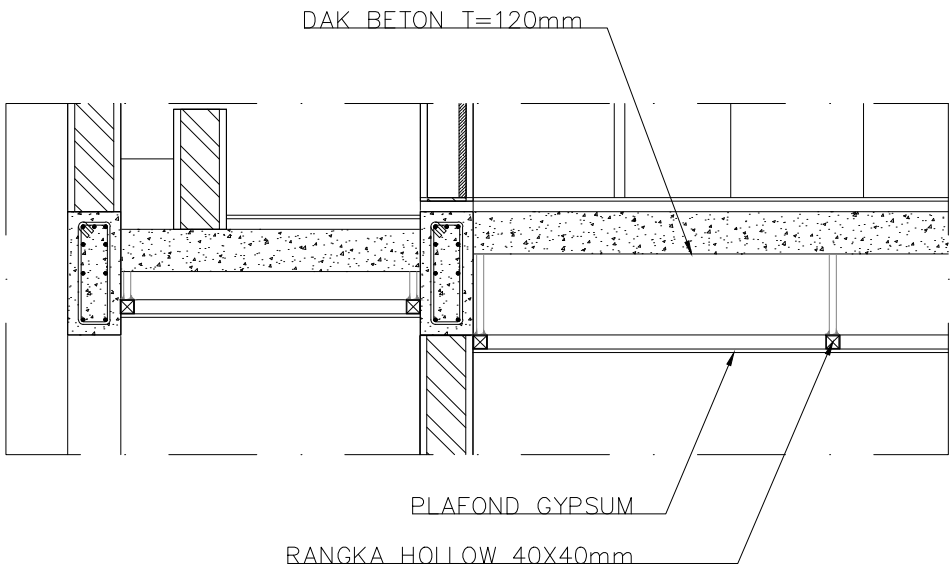


CL
ARS
POTONGAN A-A
1:15

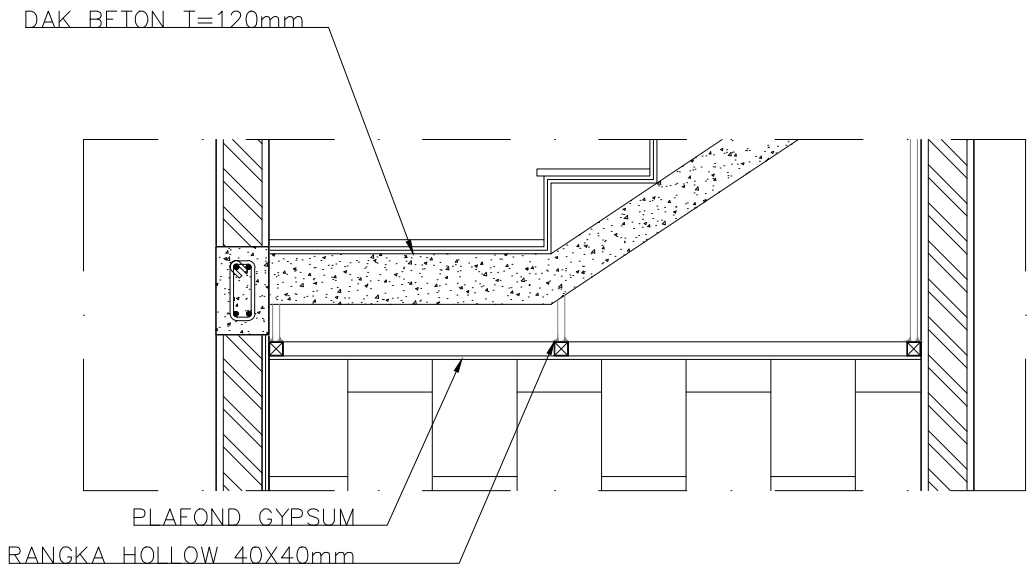

CL
ARS
POTONGAN B-B
1:15

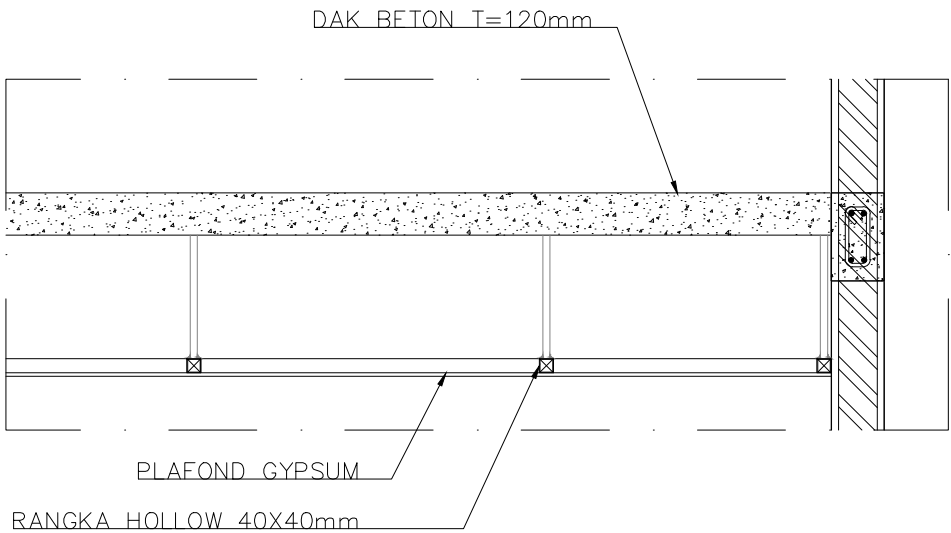


CL
ARS
POTONGAN C-C
1:15

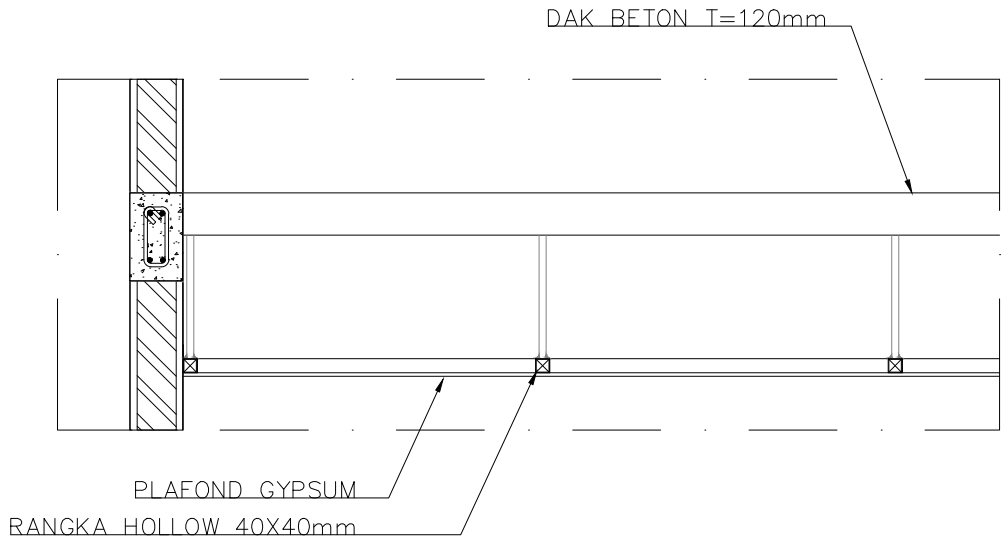


CL
ARS
POTONGAN D-D
1:15

06
ARS
TAMPAK SAMPIK KIRI
S K A L A 1 : 15

KEGIATAN :		
PEKERJAAN :		
LOKASI :		
DIBUAT OLEH :		
GAMBAR		SKALA
No. Lbr	Jml. Lbr	Kode Gambar
	-	

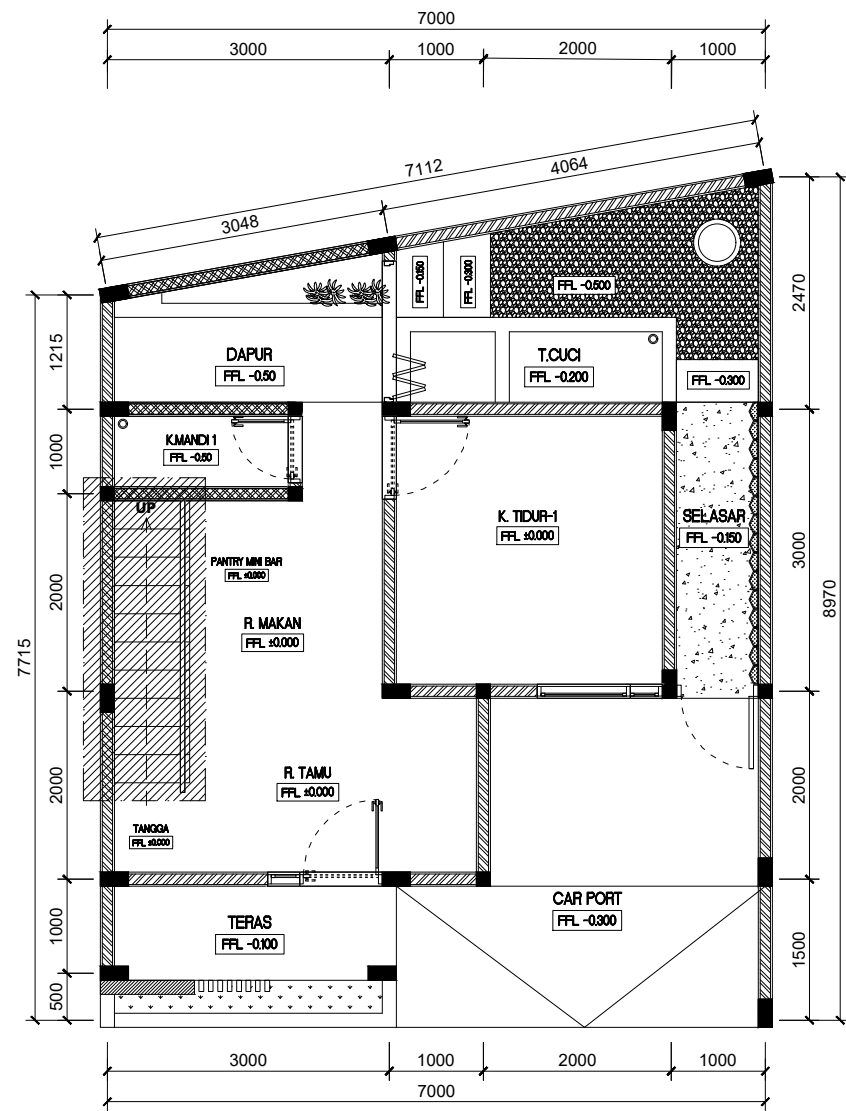

0
ARS
DENAH LT.1
1: 75

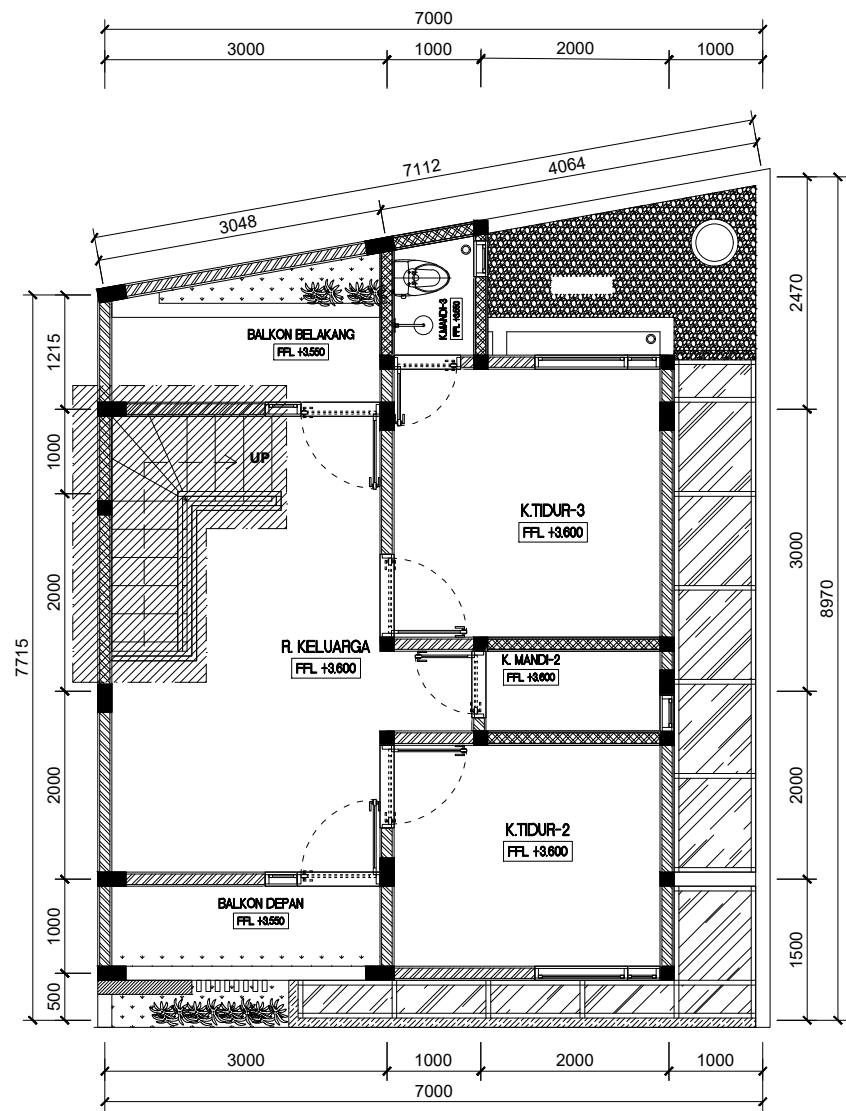

0
ARS
DENAH LT.2
1: 75

10
ARS
DENAH TANGGA
SKALA 1 : 75

KEGIATAN :




PEKERJAAN :

LOKASI :

DIBUAT OLEH :

GAMBAR SKALA

No. Lbr Jml. Lbr Kode Gambar

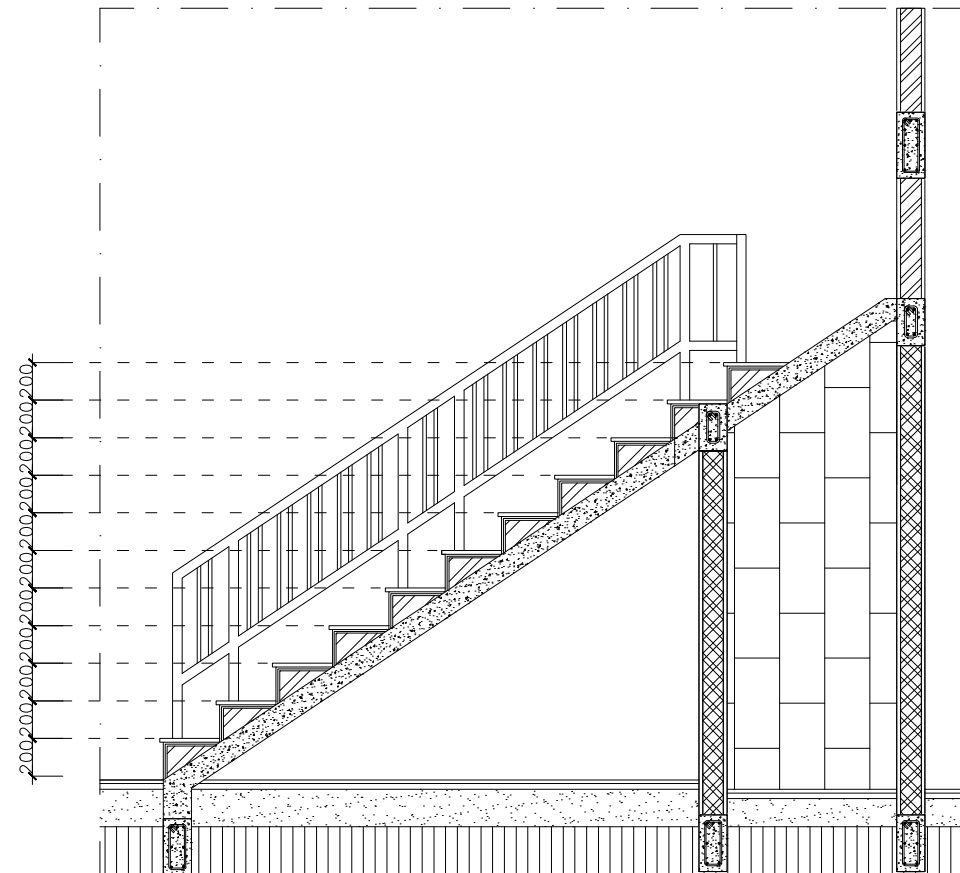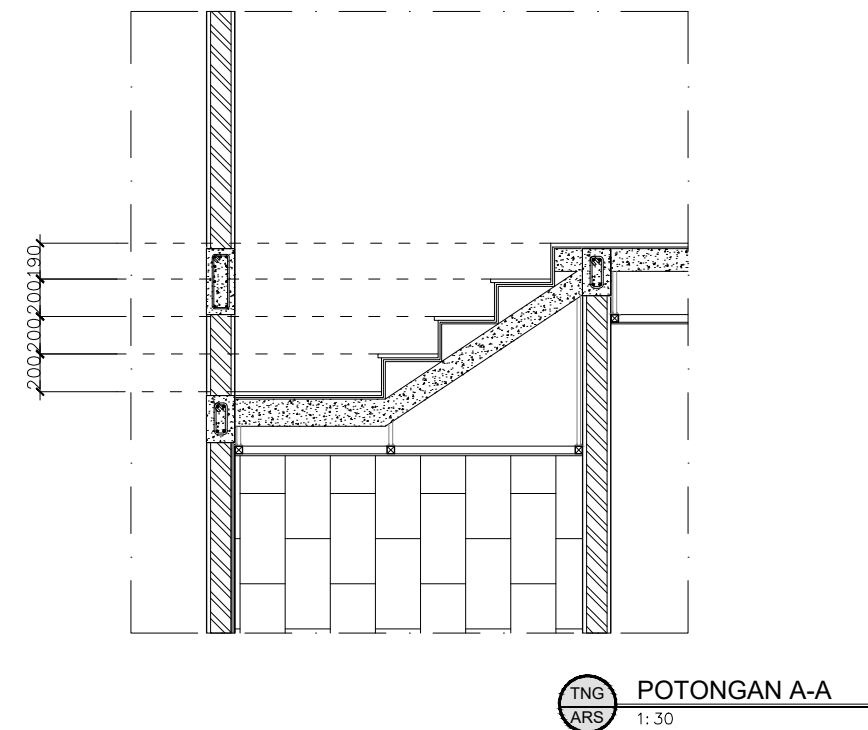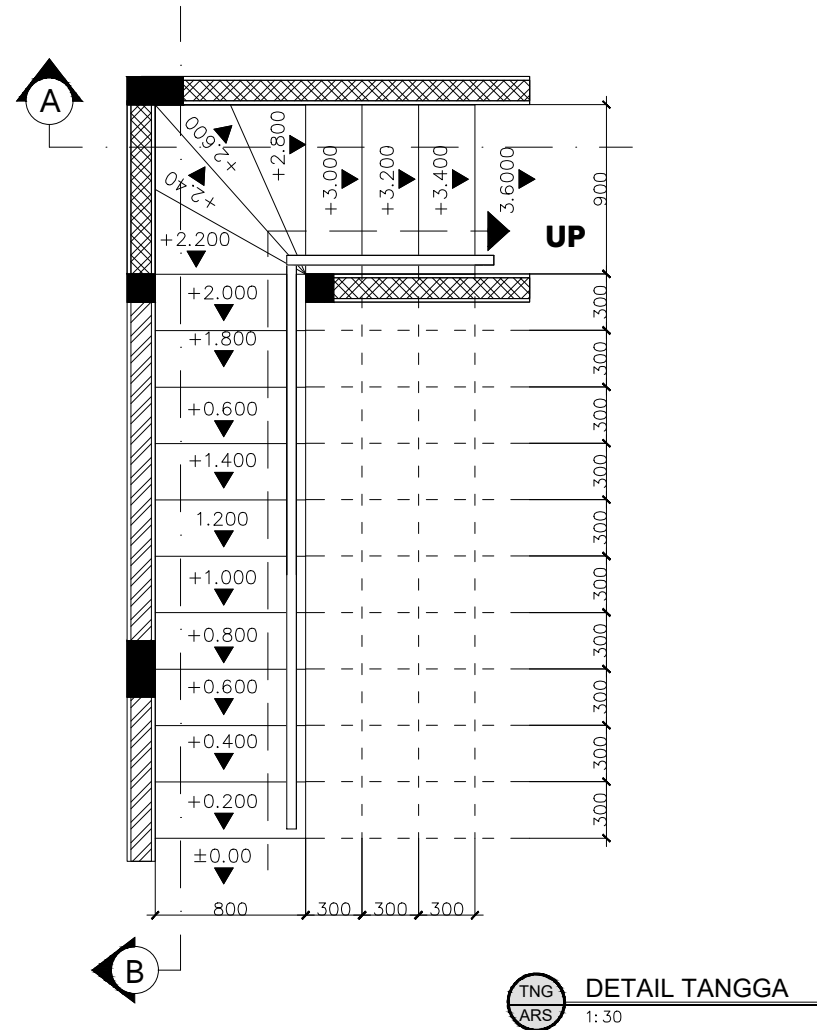

POTONGAN B-B
1:30

DETAIL TANGGA
SKALA 1:30

KEGIATAN :

PEKERJAAN :

LOKASI :

DIBUAT OLEH :


GAMBAR

SKALA

No. Lbr

Jml. Lbr

Kode Gambar

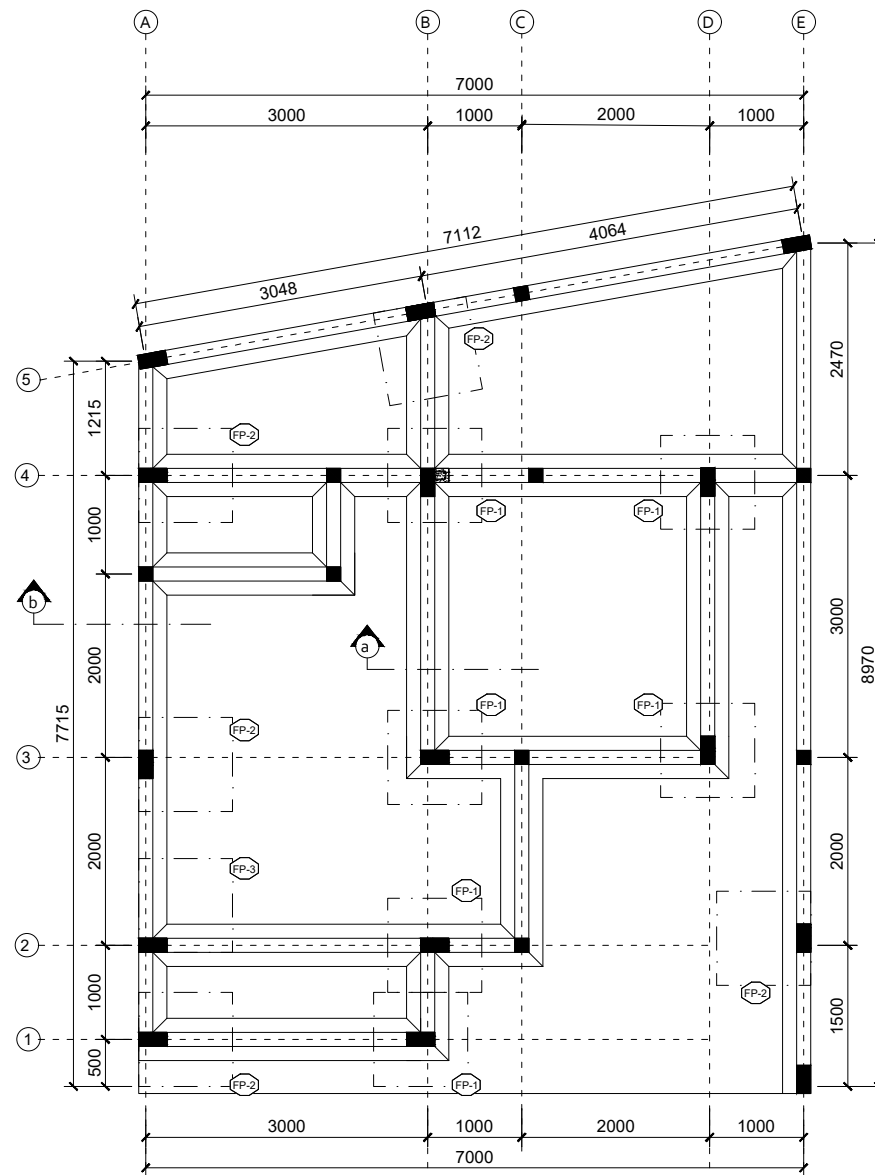

0 DENAH RENC. PONDASI
STR SKALA 1 : 75

KEGIATAN :


PEKERJAAN :

LOKASI :


DIBUAT OLEH :

GAMBAR SKALA


No. Lbr	Jml. Lbr	Kode Gambar
	-	

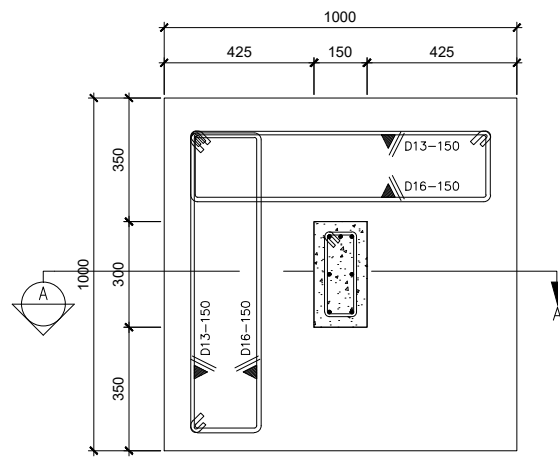


2
STR
DETAIL FP-1
1: 20

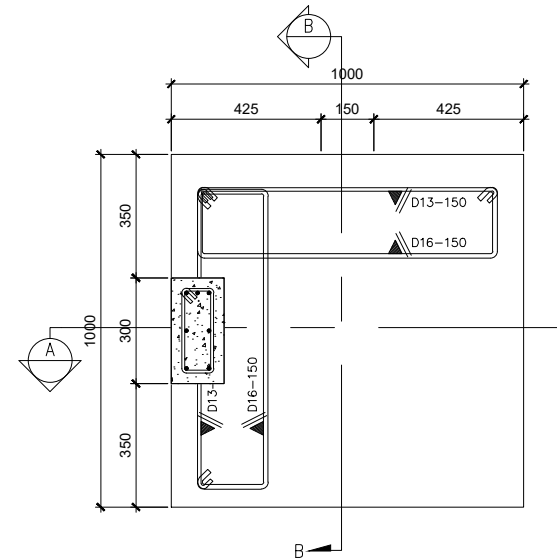

2
STR
DETAIL FP-2
1: 20

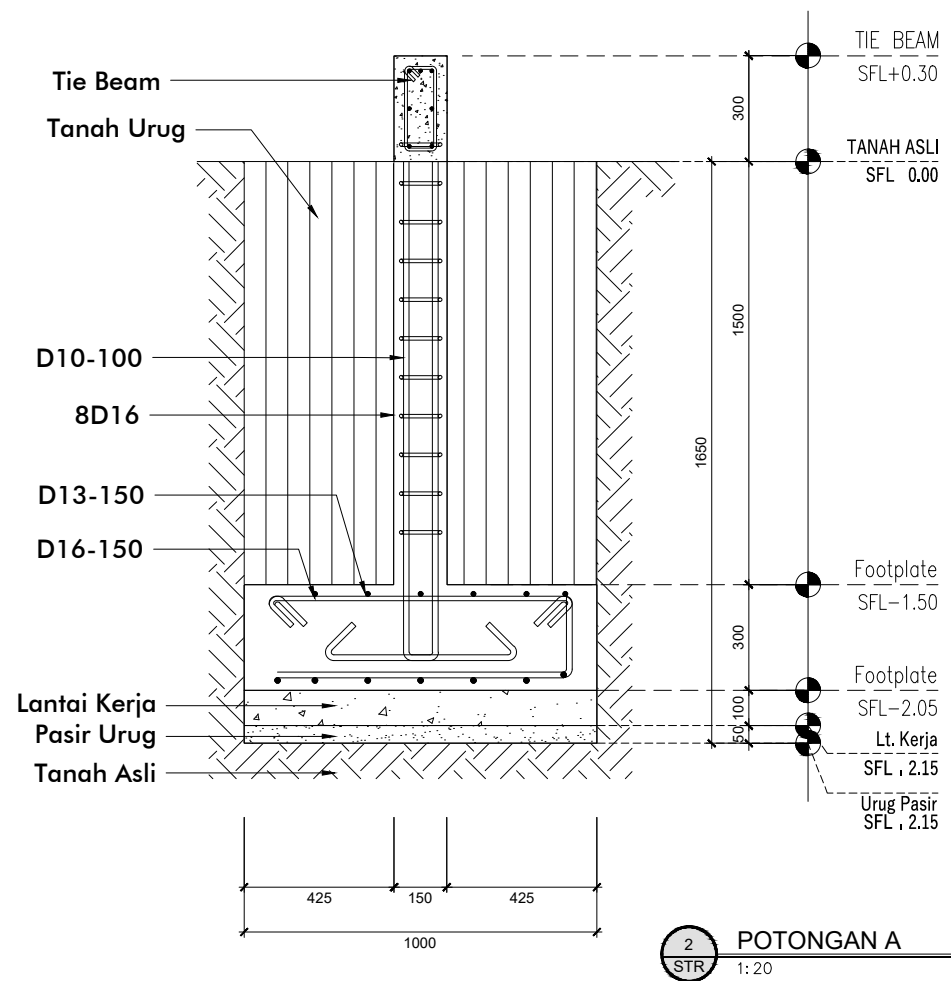

2
STR
POTONGAN A
1: 20

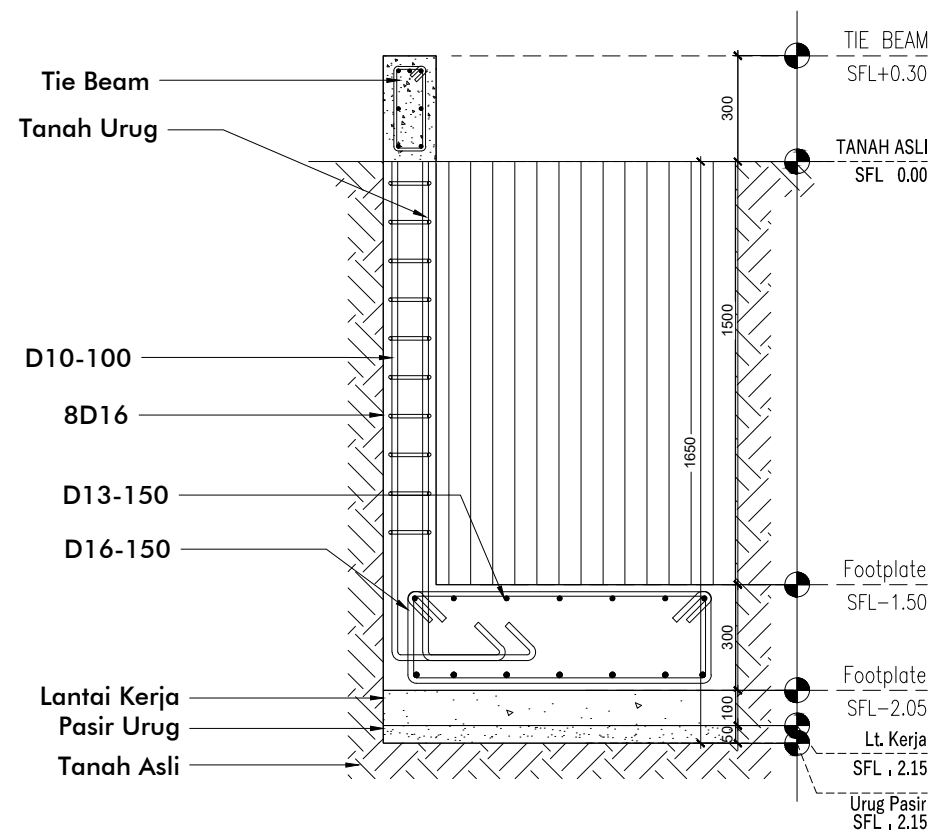

2
STR
POTONGAN A
1: 20

06
ARS
TAMPAK SAMPIING KIRI
S K A L A 1 : 15

KEGIATAN :

PEKERJAAN :

LOKASI :

DIBUAT OLEH :


GAMBAR

SKALA


No. Lbr

Jml. Lbr


Kode Gambar

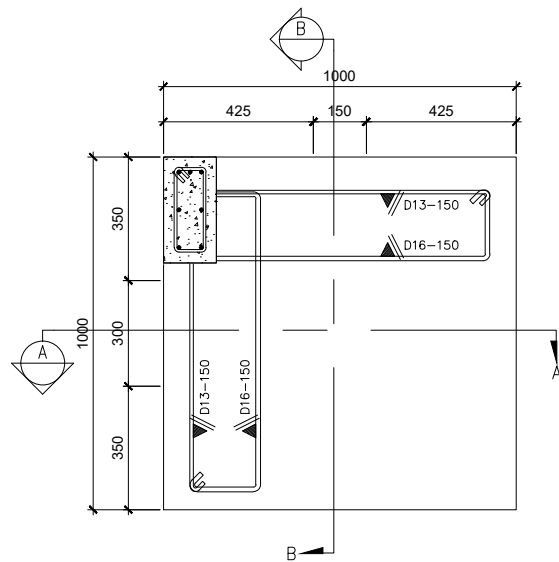


2
STR
DETAIL FP-3
1: 20

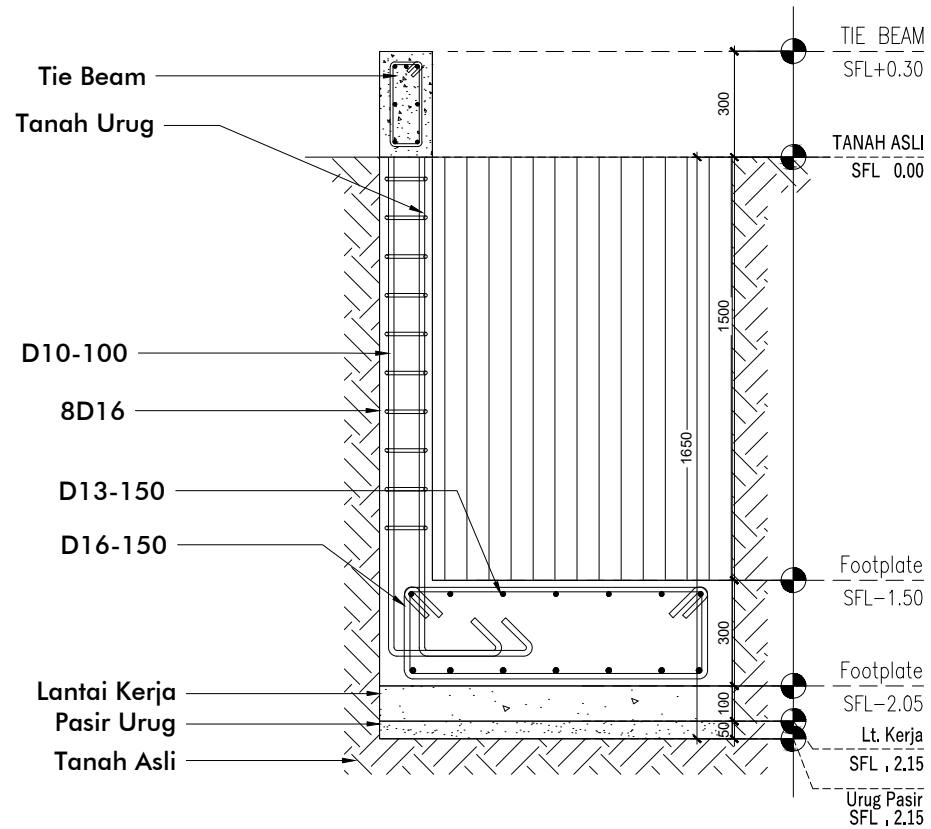

2
STR
POTONGAN A
1: 20

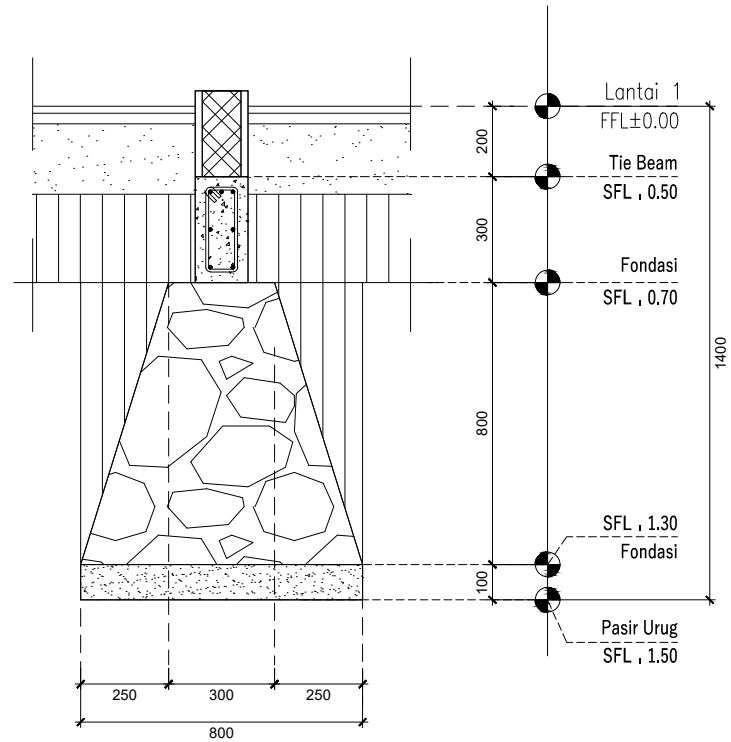

2
STR
POTONGAN a-a
1: 20

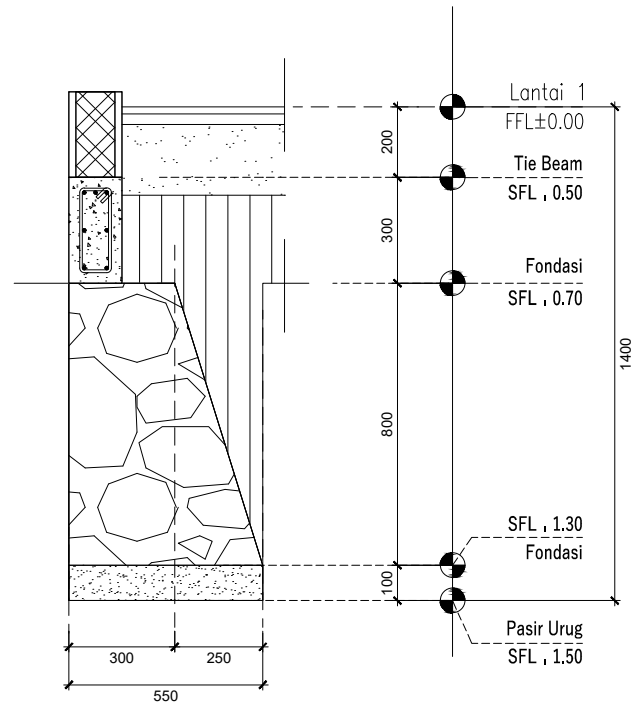

2
STR
POTONGAN b-b
1: 20

06
ARS
TAMPAK SAMPING KIRI
S K A L A 1 : 15

KEGIATAN :

PEKERJAAN :

LOKASI :

DIBUAT OLEH :

GAMBAR


SKALA

No. Lbr

Jml. Lbr

Kode Gambar


NOTASI	KETERANGAN
SLF	SLOOF 150X200 (FFL-0.500)

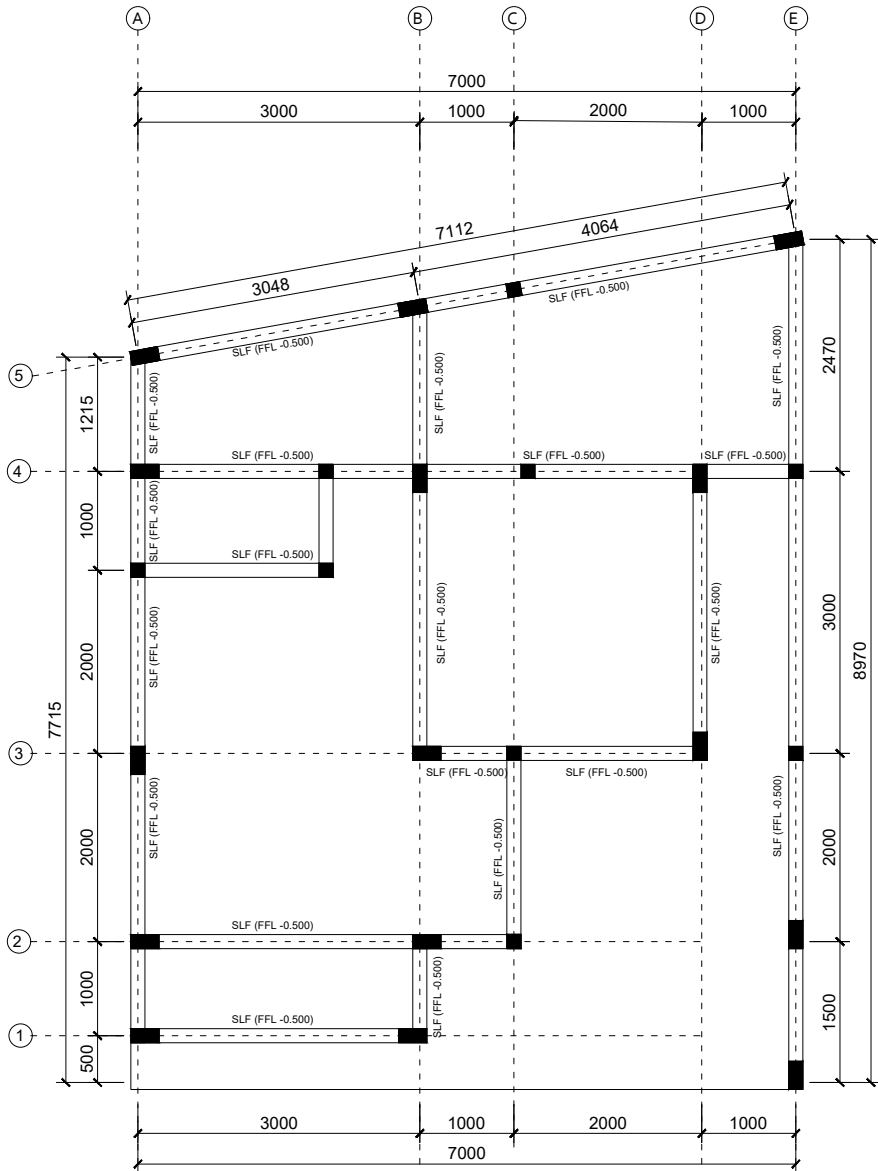


0
STR

DENAH RENC. SLOOF
SKALA 1 : 75

KEGIATAN :		
PEKERJAAN :		
LOKASI :		
DIBUAT OLEH :		
GAMBAR		SKALA
No. Lbr	Jml. Lbr	Kode Gambar
	-	

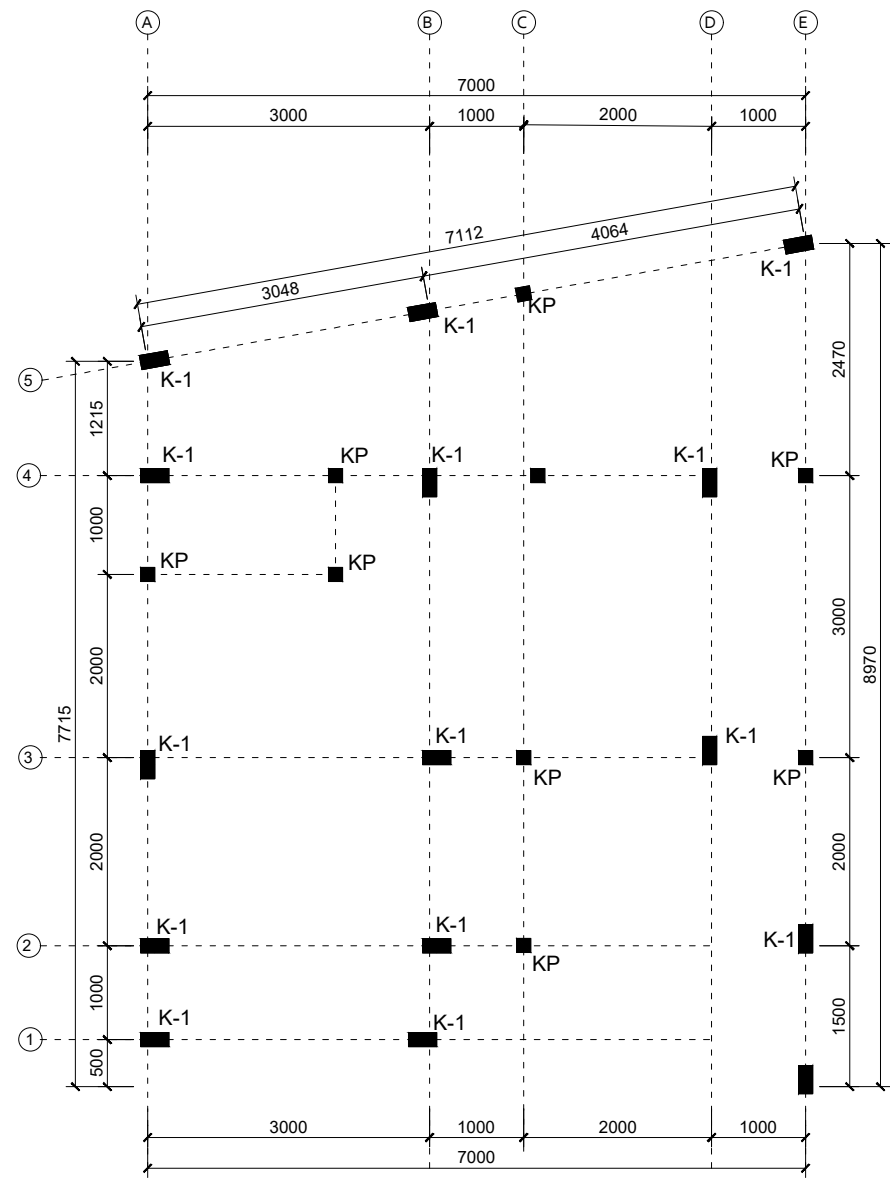

 DENAH LT.1
1: 75

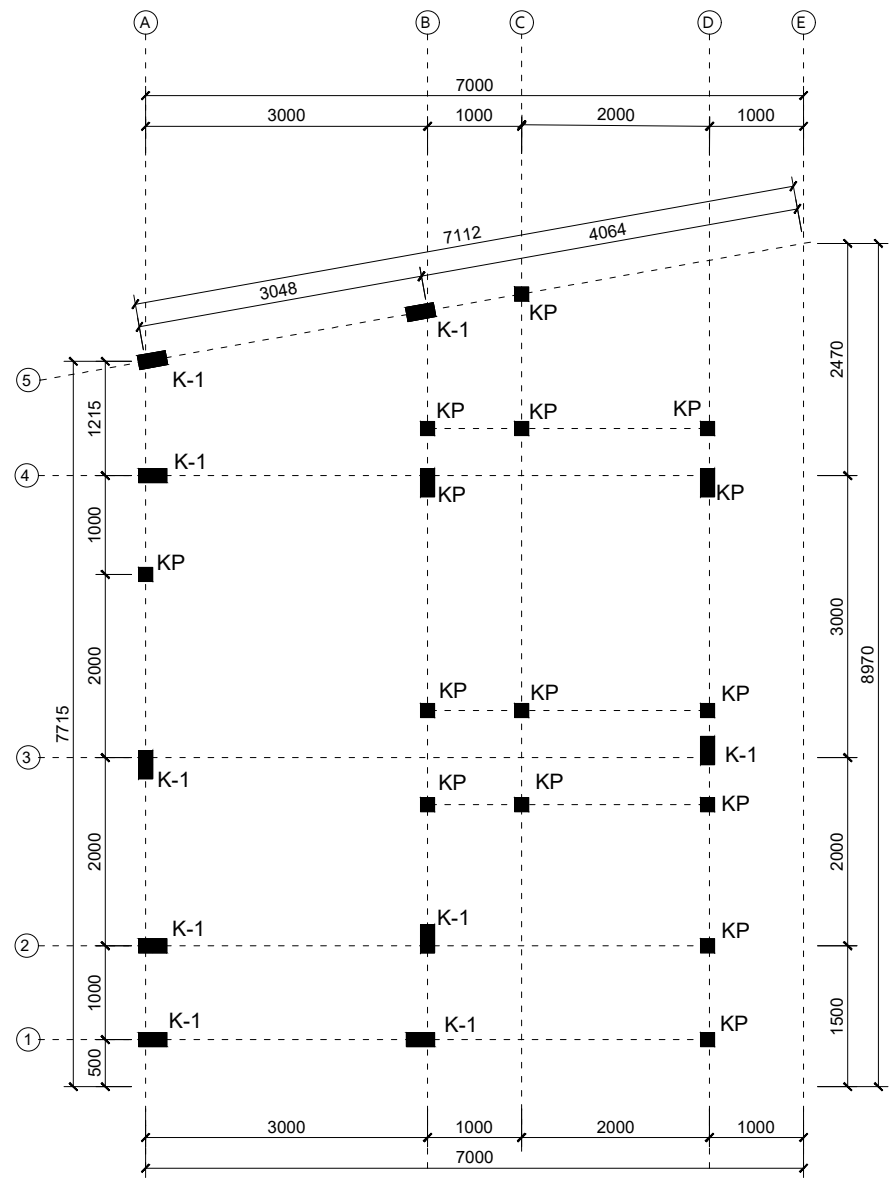

 DENAH LT.2
1: 75

NOTASI	KETERANGAN
K1	KOLOM STRUKTUR 350x150
KP	KOLOM PRAKTIS 150x150

 DENAH RENC. KOLOM
SKALA 1 : 75


KEGIATAN :

PEKERJAAN :


LOKASI :

DIBUAT OLEH :

GAMBAR		SKALA
No. Lbr	Jml. Lbr	Kode Gambar
	-	

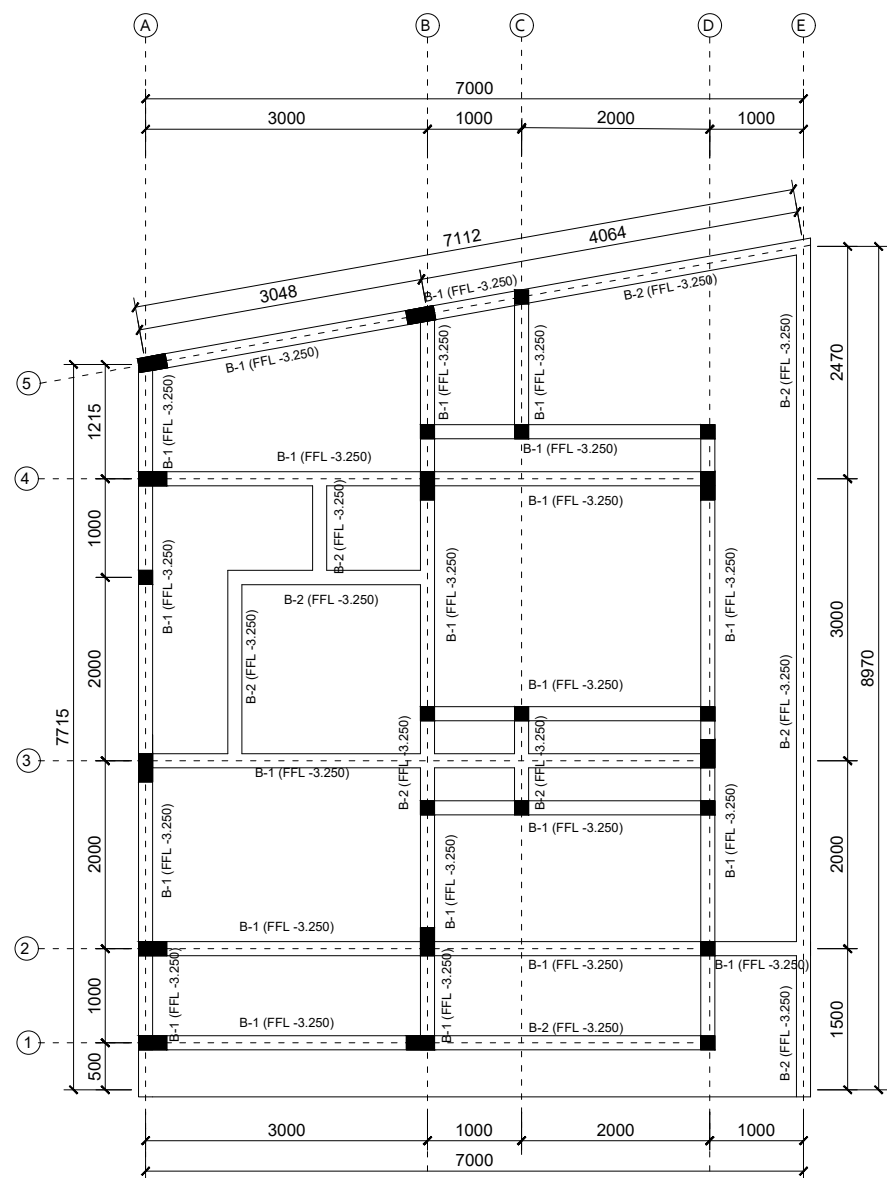

BL STR DENAH LT.1 1: 75

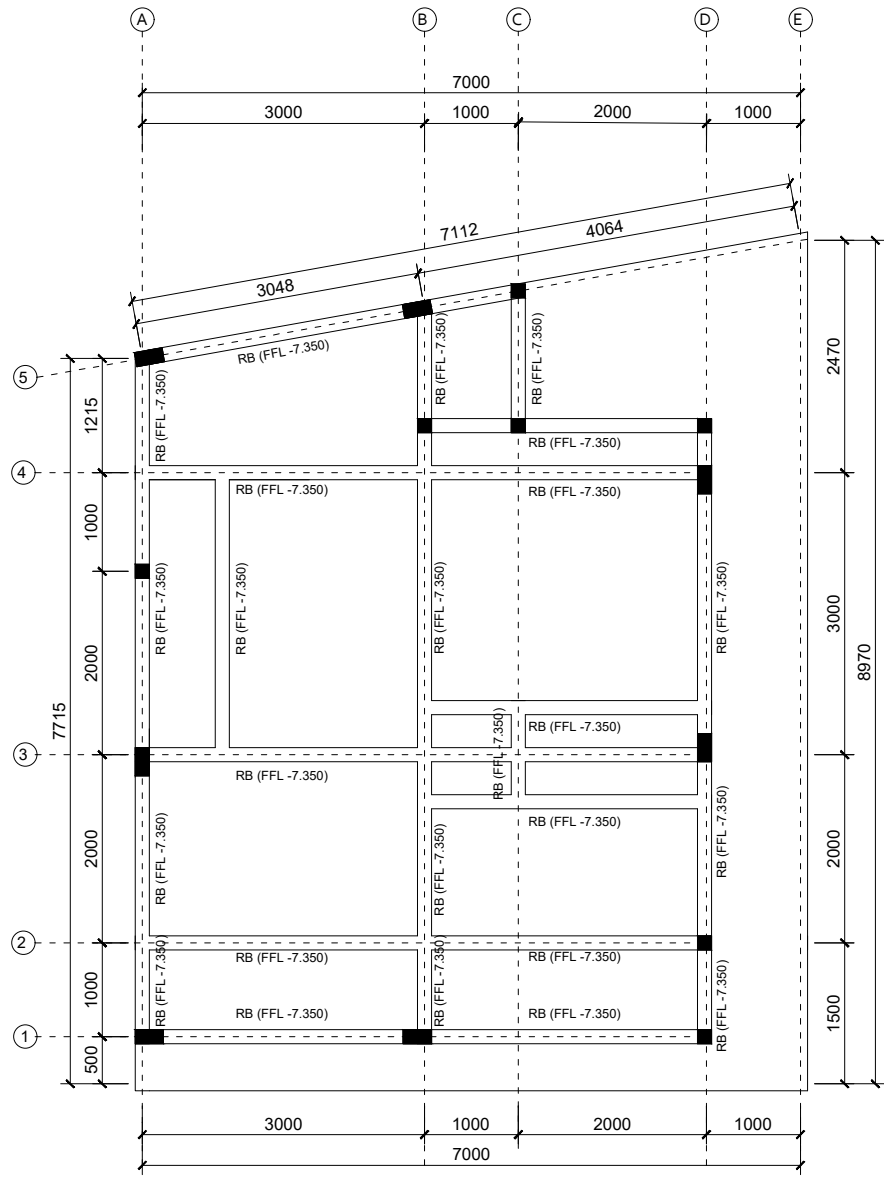


RB STR DENAH LT.2 1: 75


NOTASI	KETERANGAN
B-1	BALOK INDUK 150X350 (FFL-3.250)
B-2	BALOK ANAK 150X250 (FFL-3.250)
RB	RING BALK 150X200 (FFL-7.350)

0 STR DENAH RENC. BALOK & RINGBALK SKALA 1 : 75

KEGIATAN :		
PEKERJAAN :		
LOKASI :		
DIBUAT OLEH :		
GAMBAR		SKALA
No. Lbr	Jml. Lbr	Kode Gambar
	-	

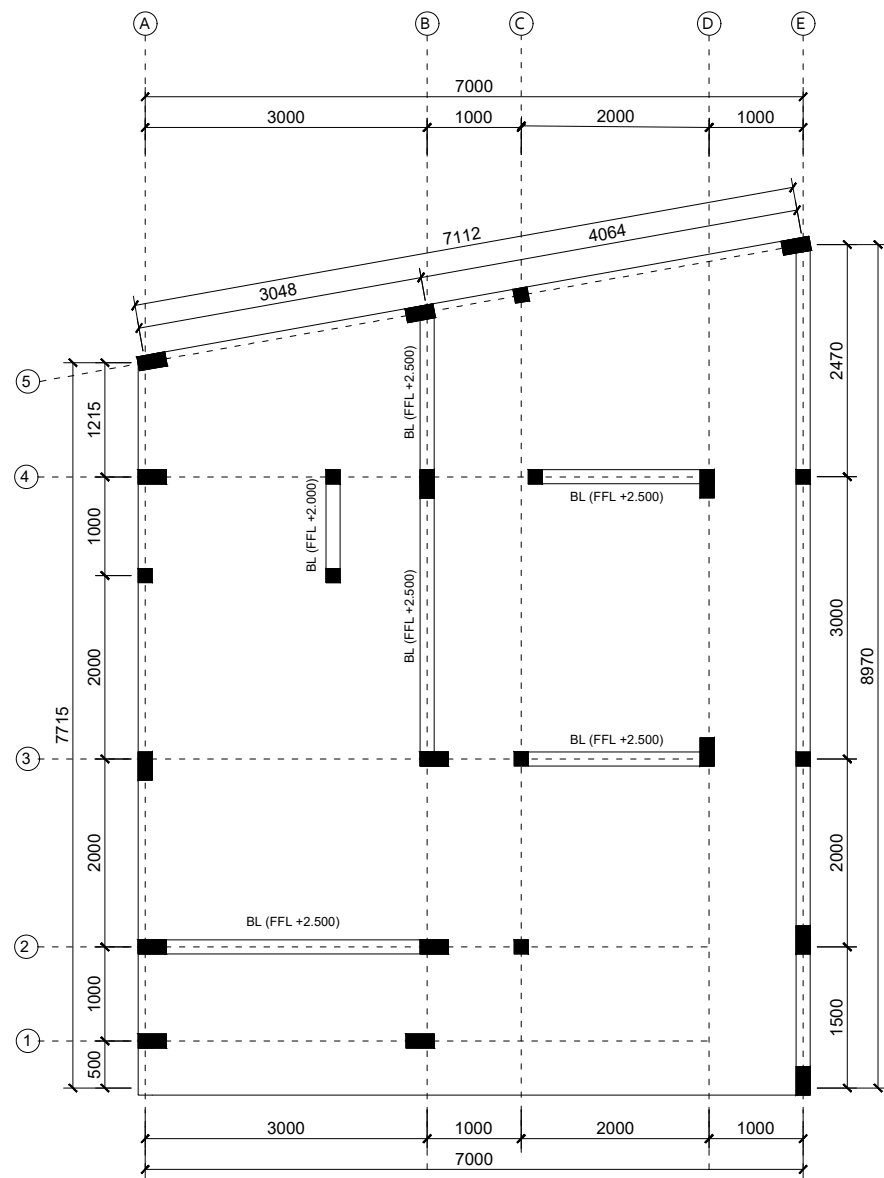

DENAH LT.1
1: 75

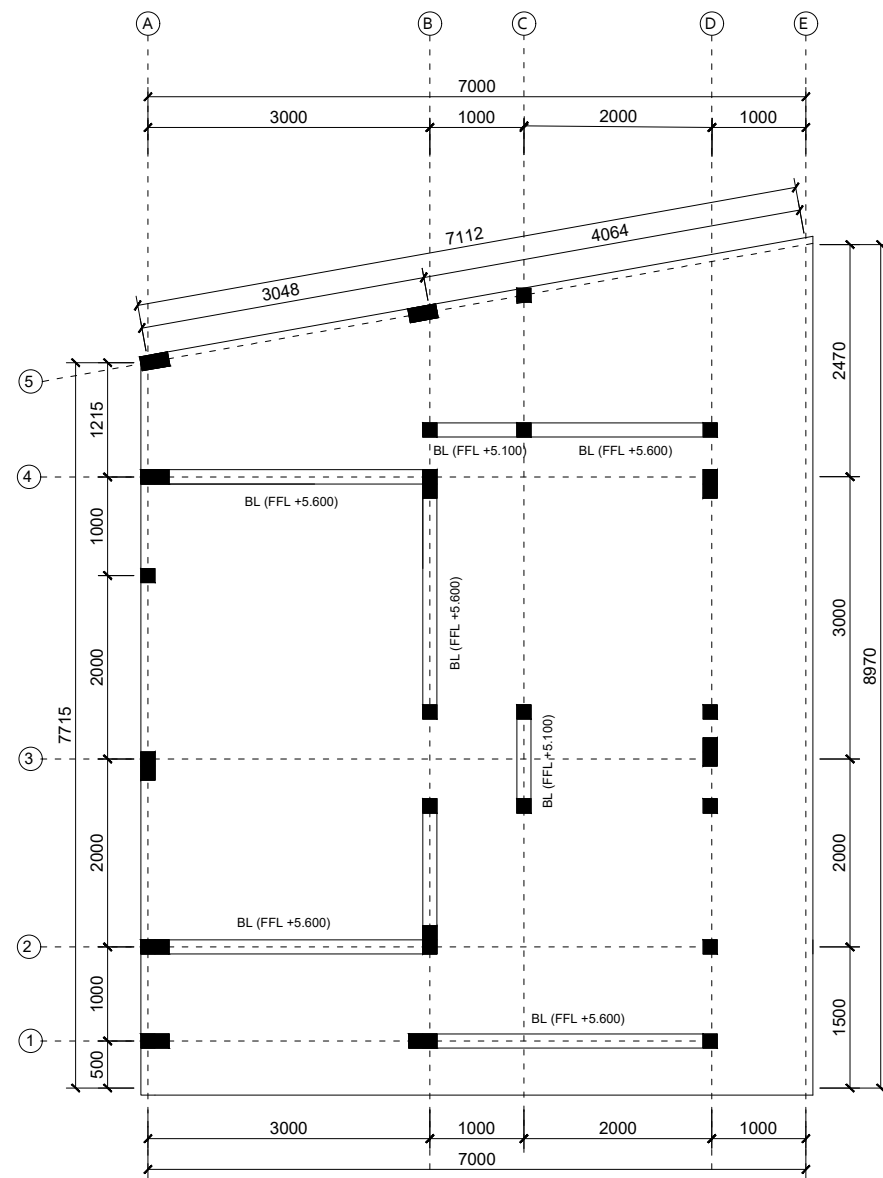

DENAH LT.2
1: 75

NOTASI	KETERANGAN
BL	BALOK LATEI 150X150

DENAH RENC. BALOK LATEI
SKALA 1 : 75

KEGIATAN :

PEKERJAAN :

LOKASI :

DIBUAT OLEH :

GAMBAR		SKALA
No. Lbr	Jml. Lbr	Kode Gambar
	-	

TYPE KOLOM	KOLOM TYPE K1		TYPE BALOK	BALOK TYPE RB	
	TUMPUAN	LAPANGAN		TUMPUAN	LAPANGAN
K1			BL		
DIMENSI	280 X 280		DIMENSI	150 x 150	
TUL.ATAS	3D16	3D16	TUL.ATAS	2D13	2D13
TUL.TENGAH	2D16	2D16	TUL.TENGAH	-	-
TUL.BAWAH	2D16	2D16	TUL.BAWAH	2D13	3D13
TUL.SENGKANG	D10-100	D10-150	TUL.SENGKANG	D8-150	D8-150
SELIMUT BETON	30	30	SELIMUT BETON	25	25

9

ARS

DETAIL PENAMPANG KOLOM

1:10

TYPE BALOK	BALOK TYPE TIE BEAM	
	TUMPUAN	LAPANGAN
TIE BEAM		
DIMENSI	150 x 200	
TUL.ATAS	3D10	2D10
TUL.TENGAH	-	-
TUL.BAWAH	2D10	3D10
TUL.SENGKANG	P8-100	P8-150
SELIMUT BETON	30	30

9

ARS

DETAIL PENAMPANG SLOOF

1:10

TYPE BALOK	BALOK TYPE B1		TYPE BALOK	BALOK TYPE B2	
	TUMPUAN	LAPANGAN		TUMPUAN	LAPANGAN
B1			B2		
DIMENSI	250 x 350		DIMENSI	150 x 250	
TUL.ATAS	5D13	3D13	TUL.ATAS	2D13	2D13
TUL.TENGAH	-	-	TUL.TENGAH	-	-
TUL.BAWAH	3D13	5D13	TUL.BAWAH	2D13	2D13
TUL.SENGKANG	D10-100	D10-150	TUL.SENGKANG	D10-100	D10-150
SELIMUT BETON	40	40	SELIMUT BETON	40	40
TYPE BALOK	BALOK TYPE B2		TYPE BALOK	BALOK TYPE RB	
	TUMPUAN	LAPANGAN		TUMPUAN	LAPANGAN
B2			BL		
DIMENSI	150 x 250		DIMENSI	150 x 150	
TUL.ATAS	2D13	2D13	TUL.ATAS	2D13	2D13
TUL.TENGAH	-	-	TUL.TENGAH	-	-
TUL.BAWAH	2D13	2D13	TUL.BAWAH	2D13	3D13
TUL.SENGKANG	D10-100	D10-150	TUL.SENGKANG	D8-150	D8-150
SELIMUT BETON	40	40	SELIMUT BETON	25	25

10

ARS

DETAIL PENAMPANG BALOK

1:10

06

STR

DETAIL PENULANGAN

SKALA 1 : 10

KEGIATAN :


PEKERJAAN :

LOKASI :

DIBUAT OLEH :

GAMBAR SKALA


No. Lbr Jml. Lbr Kode Gambar

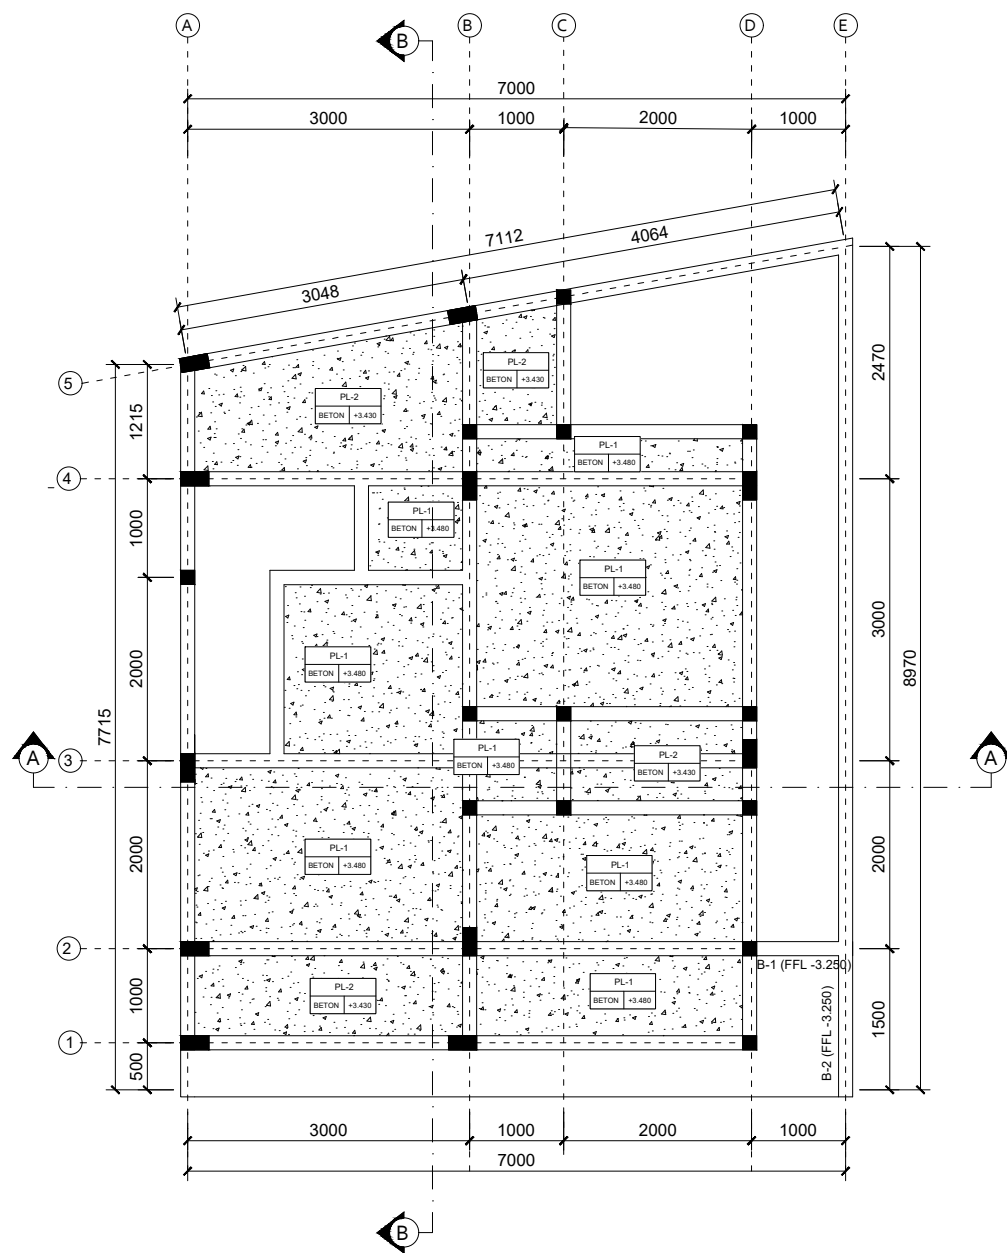

NOTASI	KETERANGAN
PL-1	PLAT LANTAI T=12cm (FFL +3.480)
PL-2	PLAT LANTAI T=12cm (FFL +3.430)

0 DENAH RENC. PLAT LANTAI
STR SKALA 1 : 75

KEGIATAN :		
PEKERJAAN :		
LOKASI :		
DIBUAT OLEH :		
GAMBAR		SKALA
No. Lbr	Jml. Lbr	Kode Gambar
	-	

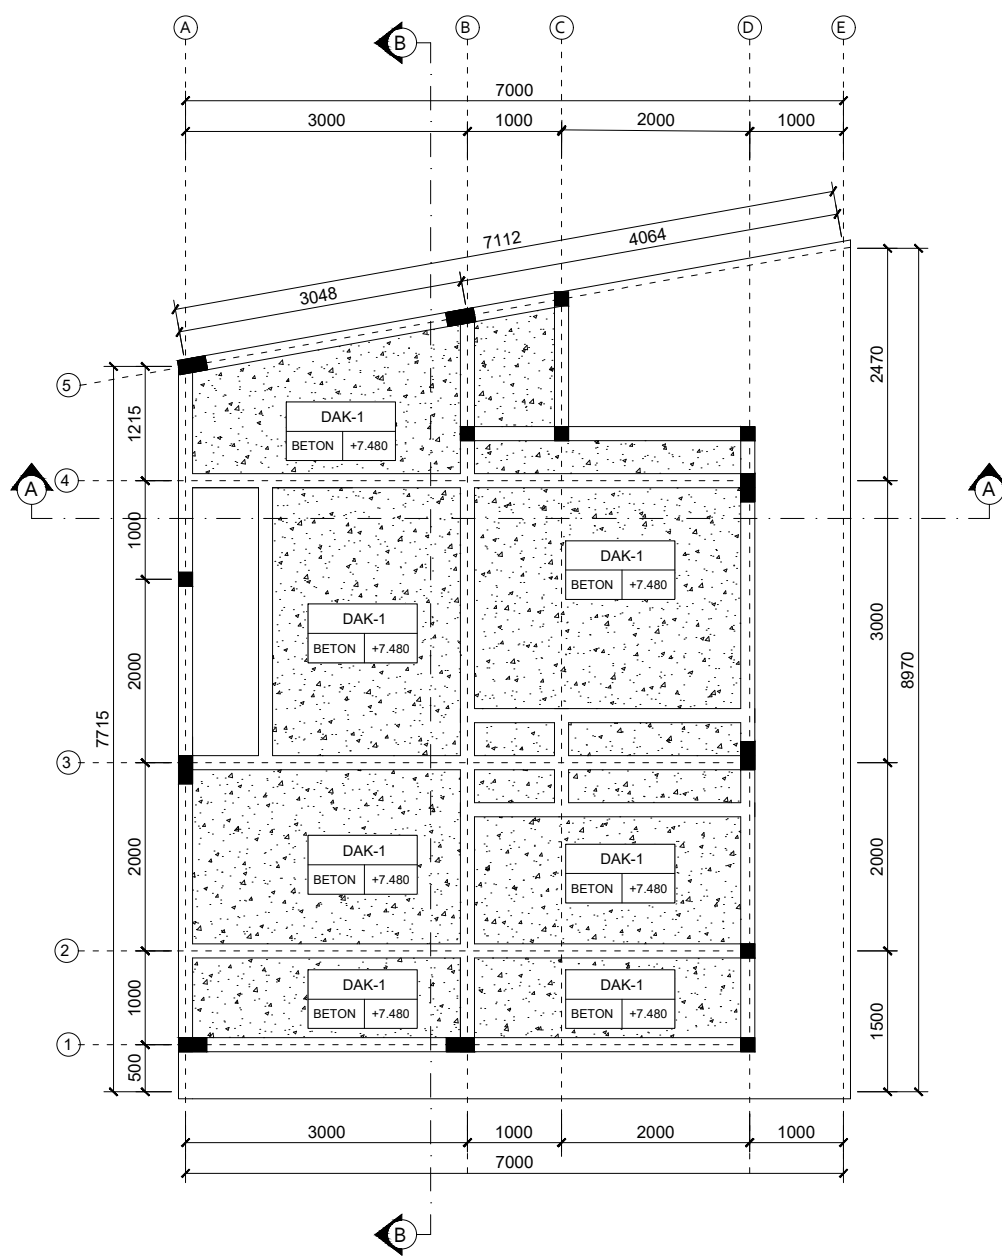


NOTASI	KETERANGAN
DAK-1	BETON DAK T=12cm (FFL +7.480)

0
STR


DENAH RENC. ATAP DAK

SKALA 1 : 75


KEGIATAN :		
PEKERJAAN :		
LOKASI :		
DIBUAT OLEH :		
GAMBAR		SKALA
No. Lbr		Kode Gambar

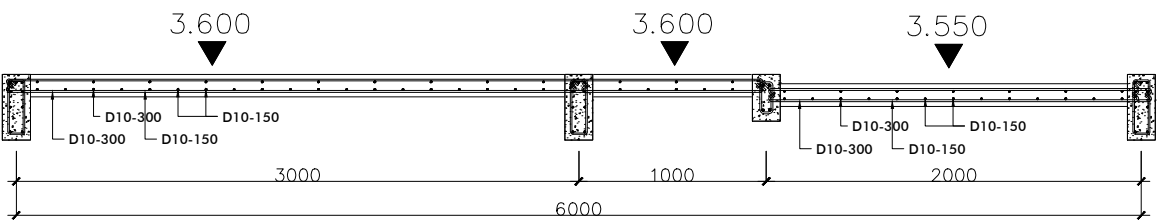

2
STR POTONGAN A-A
1: 30

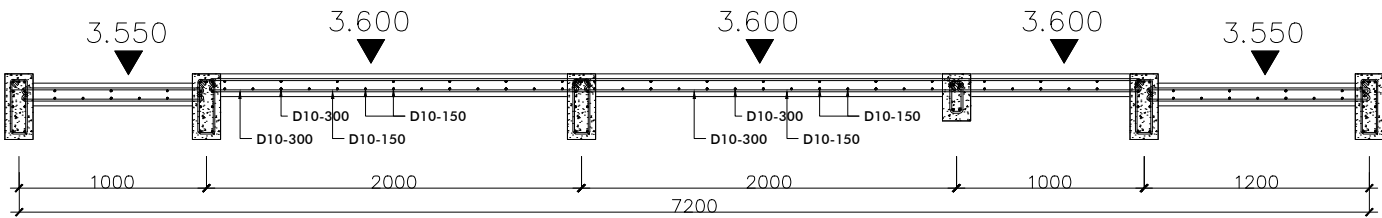

2
STR POTONGAN A-A
1: 30

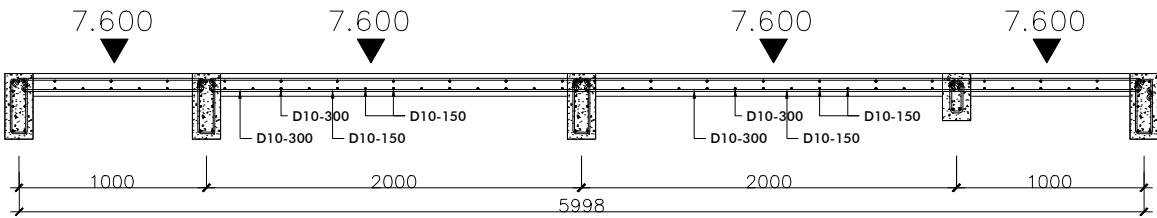

2
STR DETAIL ATAP DAK
1: 30

06
STR DETAIL PLAT LANTAI & ATAP DAK
SKALA 1 : 30

KEGIATAN :



PEKERJAAN :

LOKASI :

DIBUAT OLEH :

GAMBAR SKALA

No. Lbr	Jml. Lbr	Kode Gambar
	-	

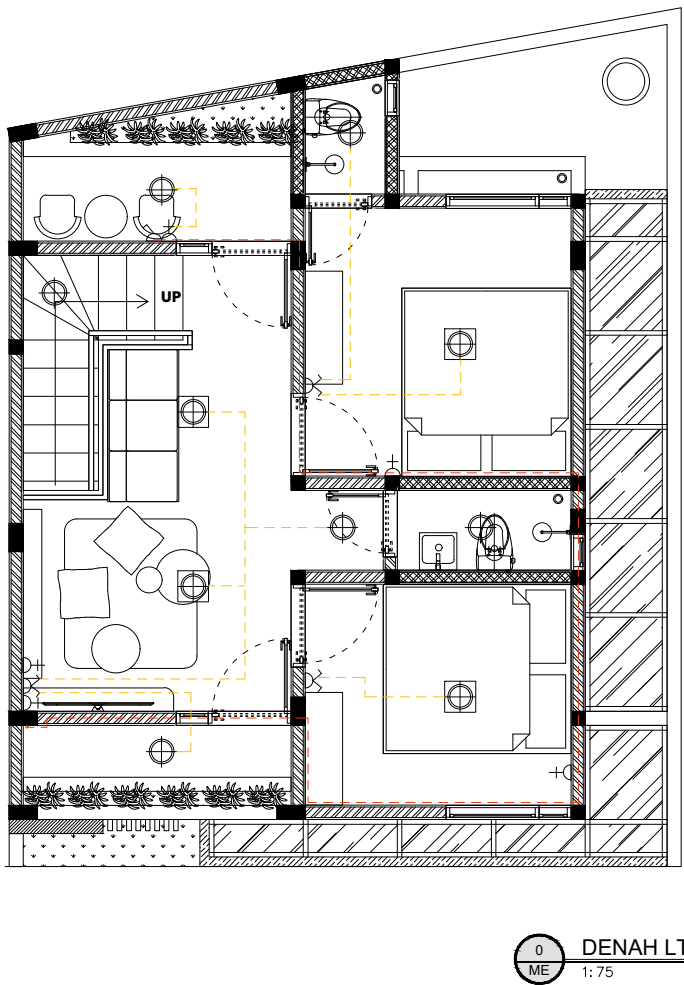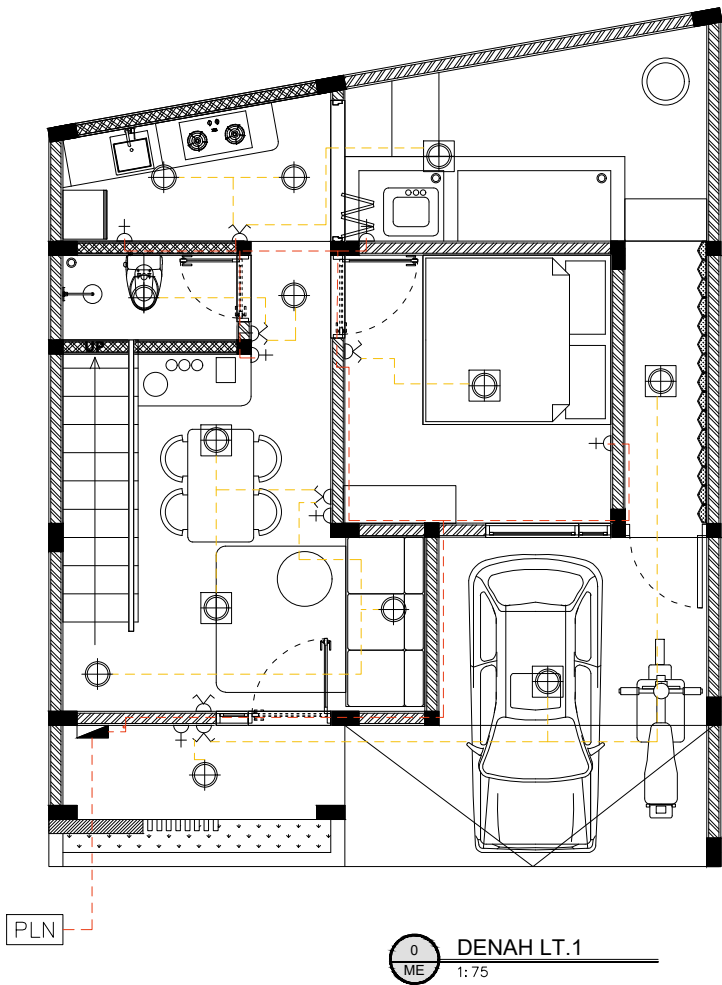


KETERANGAN

	ALUR ELEKTRIKAL UTAMA
	ALUR ELEKTRIKAL DARI SAKLAR
	DOWNLIGHT 12 WATT
	DOWNLIGHT OUTBOW 18 WATT


	SAKLAR TUNGGAL
	SAKLAR GANDA
	STOPKONTAK
	BOX PLN
	PANEL/MCB

09 DENAH ELEKTRIKAL
ME S K A L A 1 : 75

KEGIATAN :		
PEKERJAAN :		
LOKASI :		
DIBUAT OLEH :		
GAMBAR		SKALA
No. Lbr	Jml. Lbr	Kode Gambar
	-	

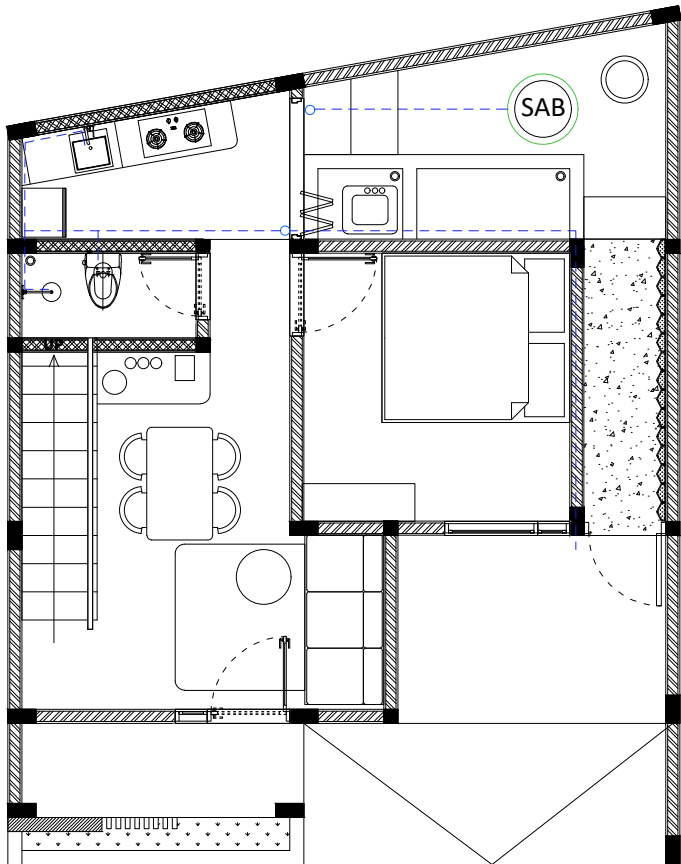

0 DENAH LT.1
ME 1:75

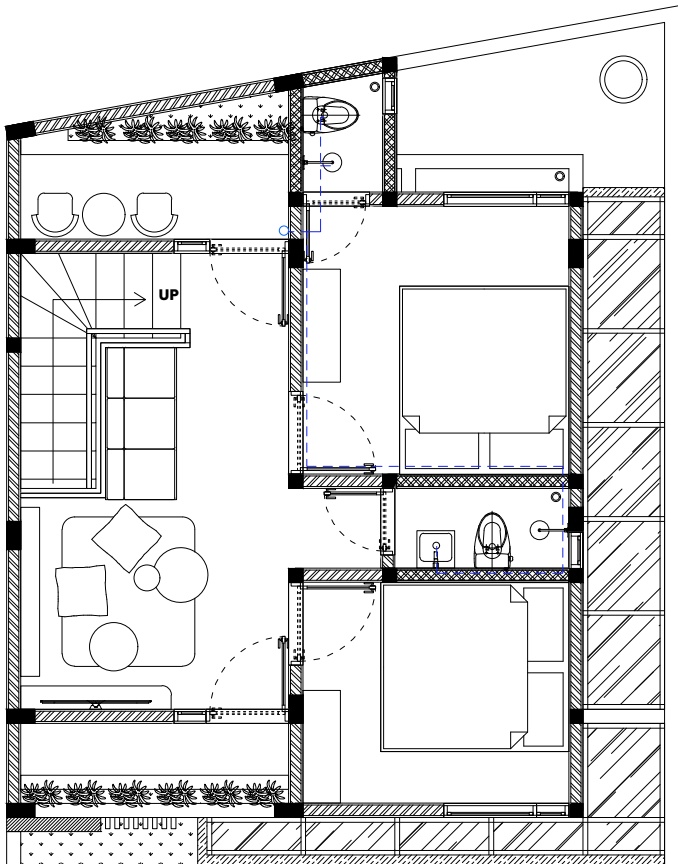

0 DENAH LT.2
ME 1:75


KETERANGAN

---	SALURAN AIR BERSIH Ø 3"
---	SALURAN AIR BERSIH NAIK Ø 3/2"
---	SALURAN AIR KOTORAN CAIR Ø 3"
---	SALURAN AIR KOTORAN PADAT Ø 4"
SR	SUMUR RESAPAN
SPAH	SALURAN PEMBUANGAN AIR HUJAN
	FLOOR DRAIN
RD	ROOF DRAIN
BK	BAK KONTROL
SP	SEPTIC TANK


T	TANDON
SAB	SUMUR AIR BERSIH
P	POMPA

09 DENAH SANITASI AIR BERSIH
ME S K A L A 1 : 7 5

KEGIATAN :		
PEKERJAAN :		
LOKASI :		
DIBUAT OLEH :		
GAMBAR		SKALA
No. Lbr	Jml. Lbr	Kode Gambar
	-	

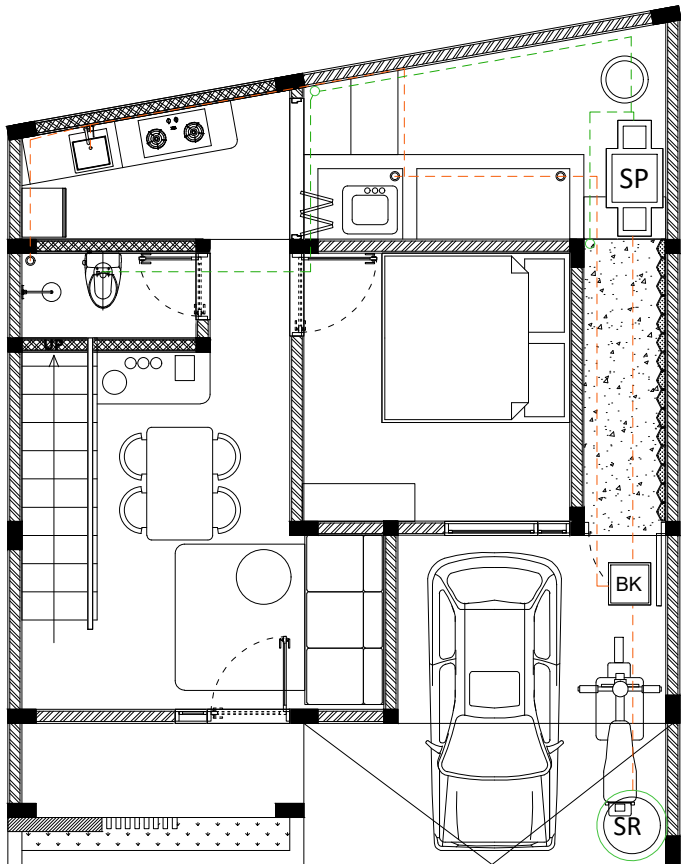

0
ME DENAH LT.1
1: 75

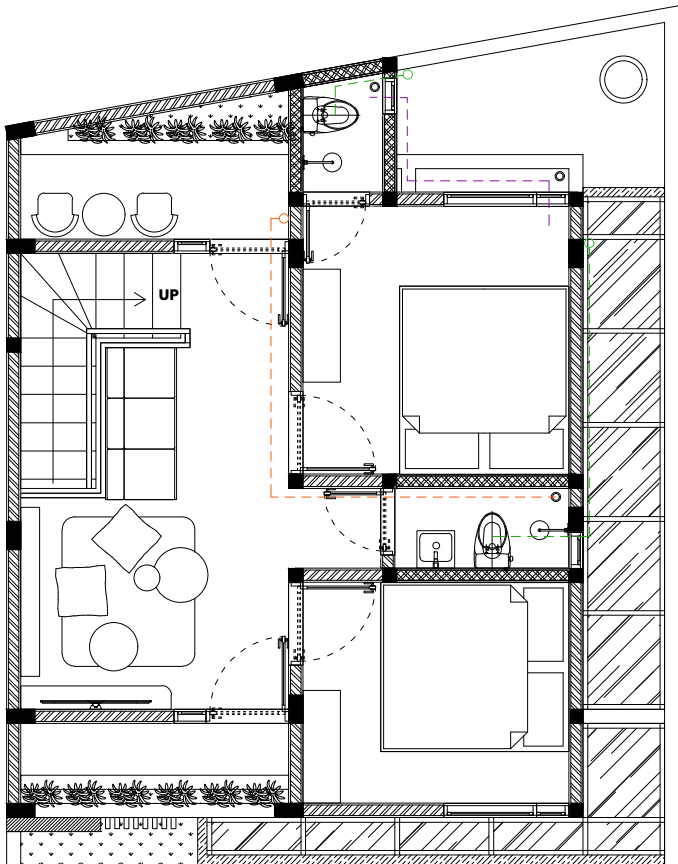

0
ME DENAH LT.2
1: 75






KETERANGAN

---	SALURAN AIR BERSIH Ø 3"
---	SALURAN AIR BERSIH NAIK Ø 3/2"
---	SALURAN AIR KOTORAN CAIR Ø 3"
---	SALURAN AIR KOTORAN PADAT Ø 4"
---	DRAINASE
SR	SUMUR RESAPAN
SPAH	SALURAN PEMBUANGAN AIR HUJAN
	FLOOR DRAIN
RD	ROOF DRAIN
BK	BAK KONTROL
SP	SEPTIC TANK


T	TANDON
SAB	SUMUR AIR BERSIH
P	POMPA

09
ME DENAH SANITASI AIR KOTOR
SKALA 1 : 75


KEGIATAN :		
PEKERJAAN :		
LOKASI :		
DIBUAT OLEH :		
GAMBAR		SKALA
No. Lbr	Jml. Lbr	Kode Gambar
	-	

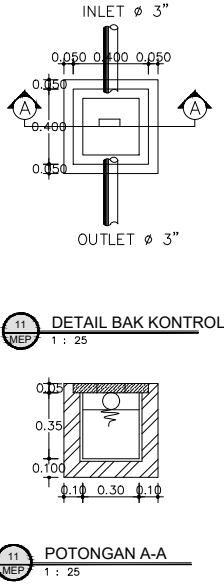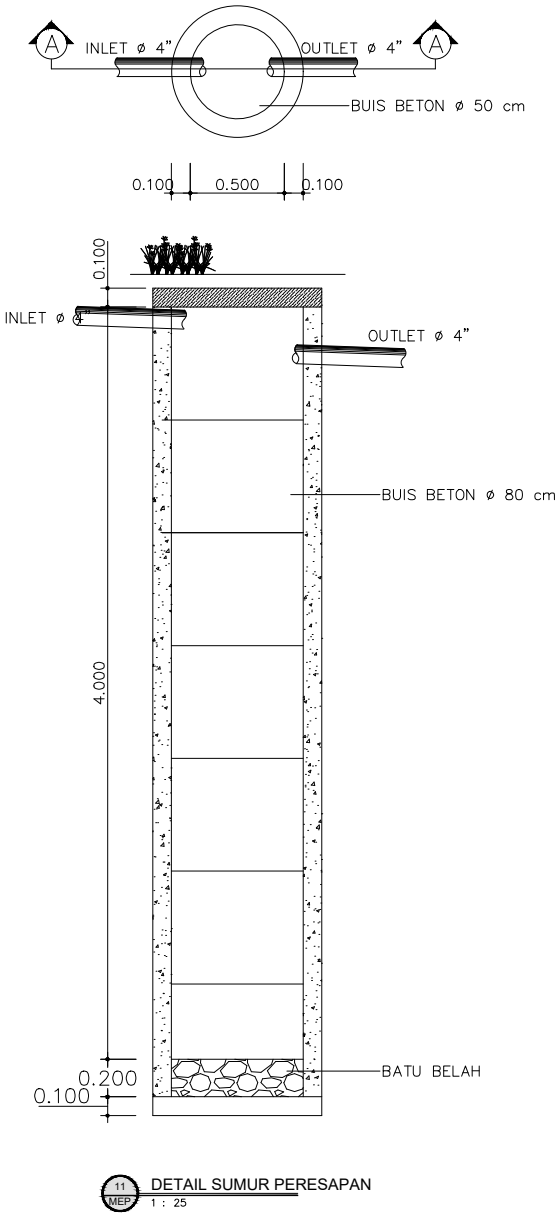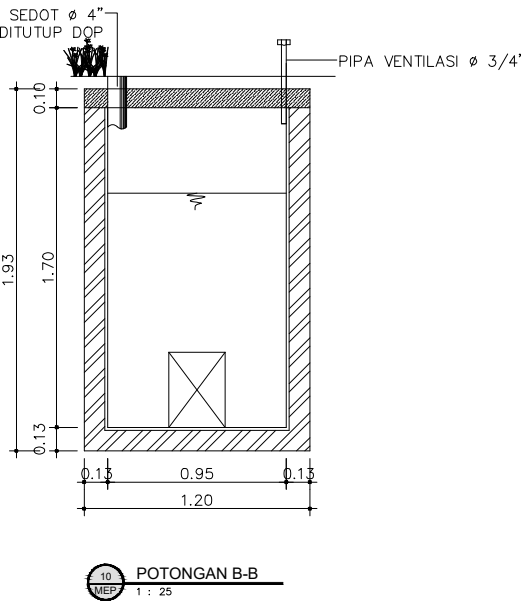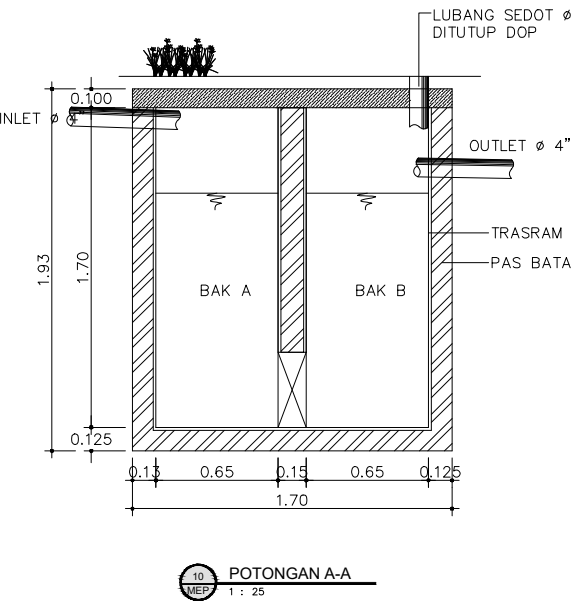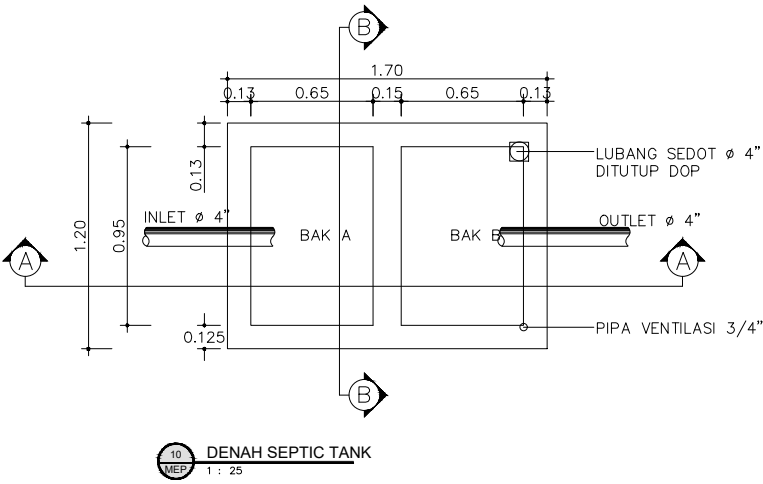

KEGIATAN :		
PEKERJAAN :		
LOKASI :		
DIBUAT OLEH :		
GAMBAR		SKALA
No. Lbr	Jml. Lbr	Kode Gambar
	-	

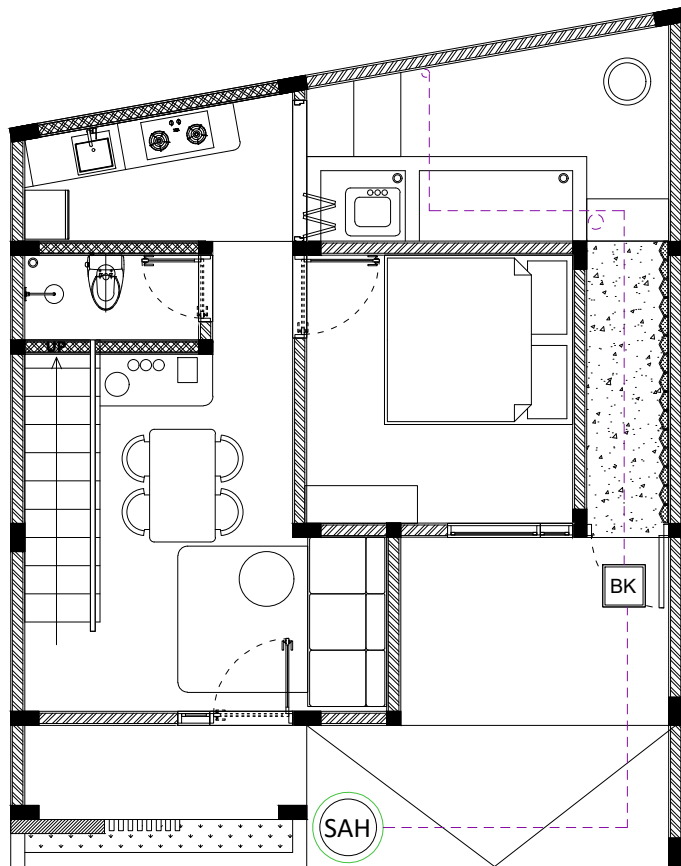

0 DENAH LT.1
ME 1:75

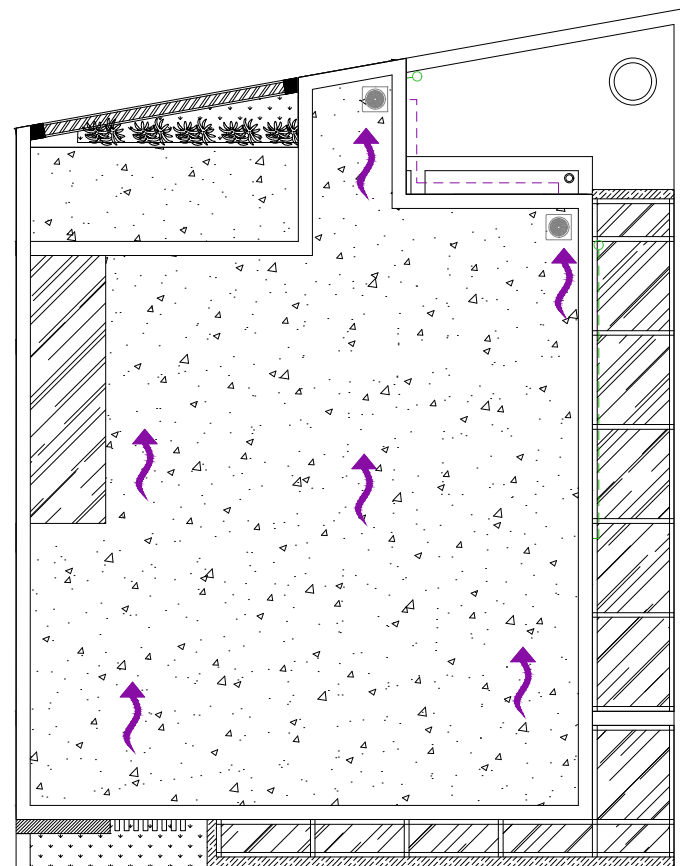

0 DENAH LT.2
ME 1:75

KETERANGAN

---	SALURAN AIR BERSIH Ø 3"
---	SALURAN AIR BERSIH NAIK Ø 3/2"
---	SALURAN AIR KOTORAN CAIR Ø 3"
---	SALURAN AIR KOTORAN PADAT Ø 4"
---	DRAINASE
SR	SUMUR RESAPAN
SPA	SALURAN PEMBUANGAN AIR HUJAN
	FLOOR DRAIN
RD	ROOF DRAIN
BK	BAK KONTROL
SP	SEPTIC TANK

T	TANDON
SAB	SUMUR AIR BERSIH
P	POMPA

09 DENAH RENC. LANTAI
ARS SKALA 1:75

KEGIATAN :

PEKERJAAN :

LOKASI :

DIBUAT OLEH :

GAMBAR SKALA

No. Lbr	Jml. Lbr	Kode Gambar
	-	